


THOANNIC


**RÉALISATION ET EXPLOITATION
D'UNE MAQUETTE NUMÉRIQUE**

CONS9 – PIÈCES GRAPHIQUES - REVIT


PRÉSENTATION DU PROJET THOANNIC

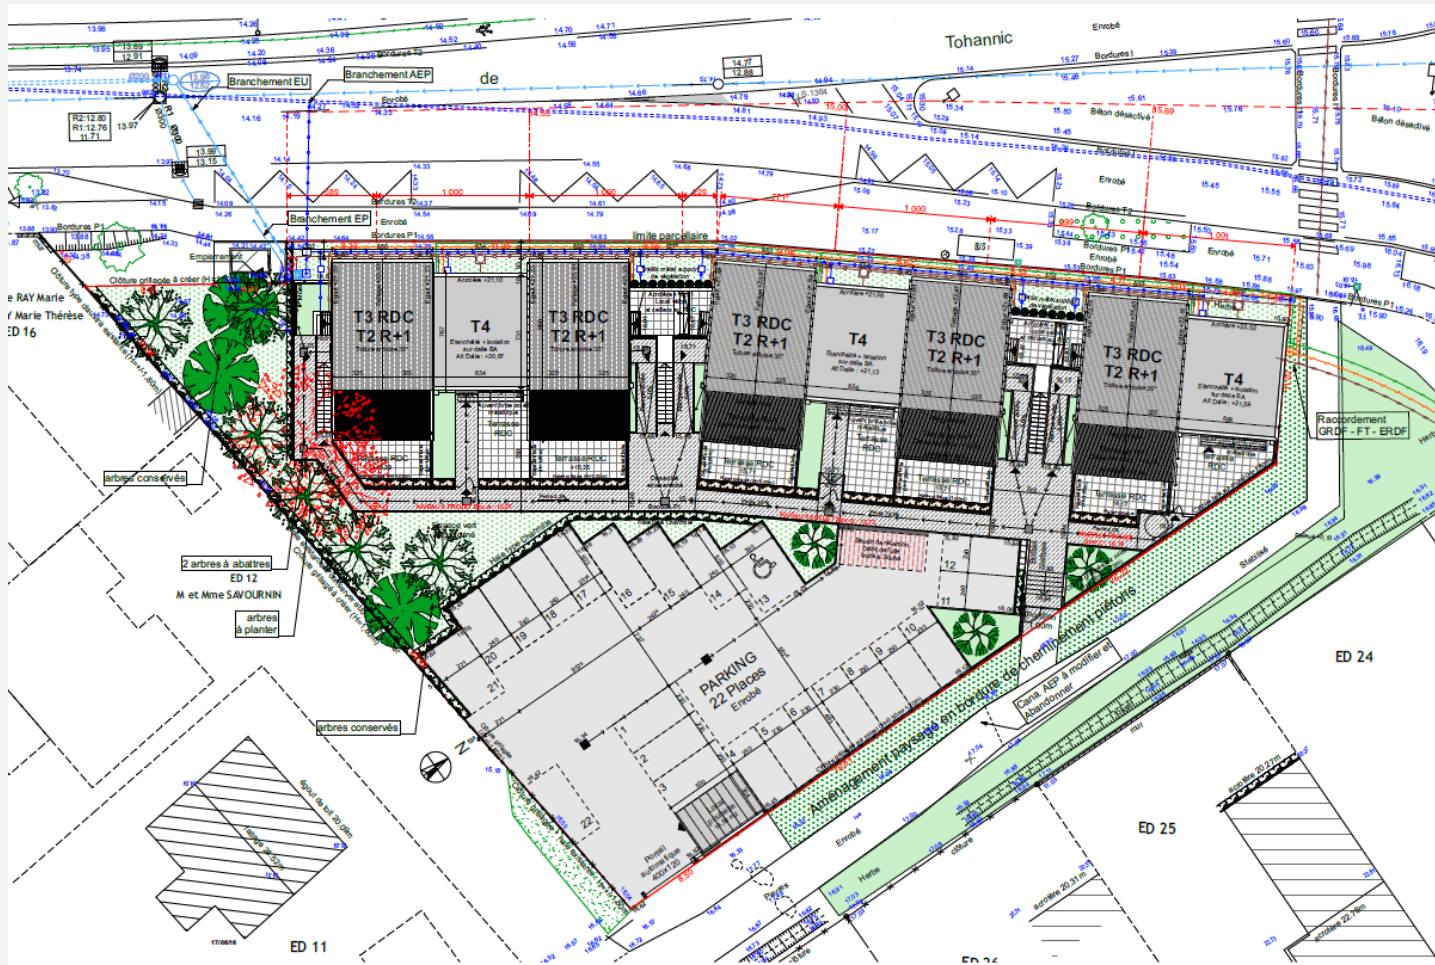


PRÉSENTATION DU PROJET THOANNIC


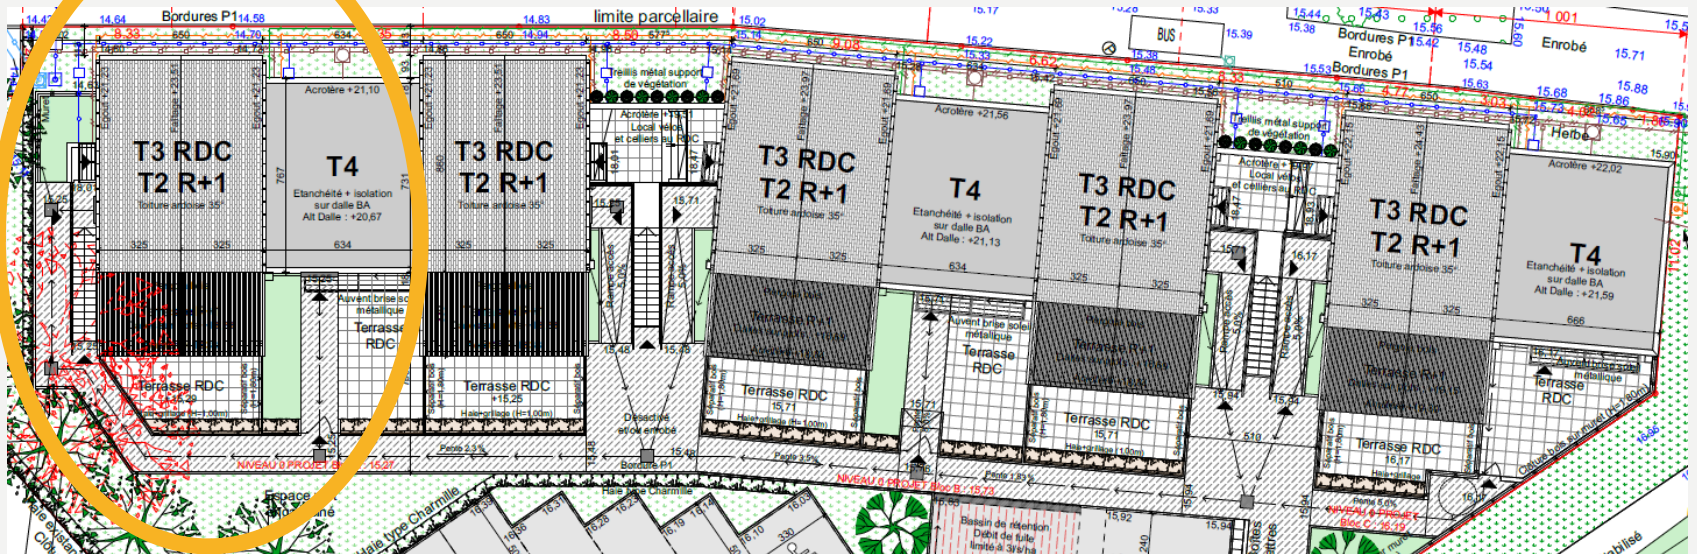


PRÉSENTATION DU PROJET THOANNIC



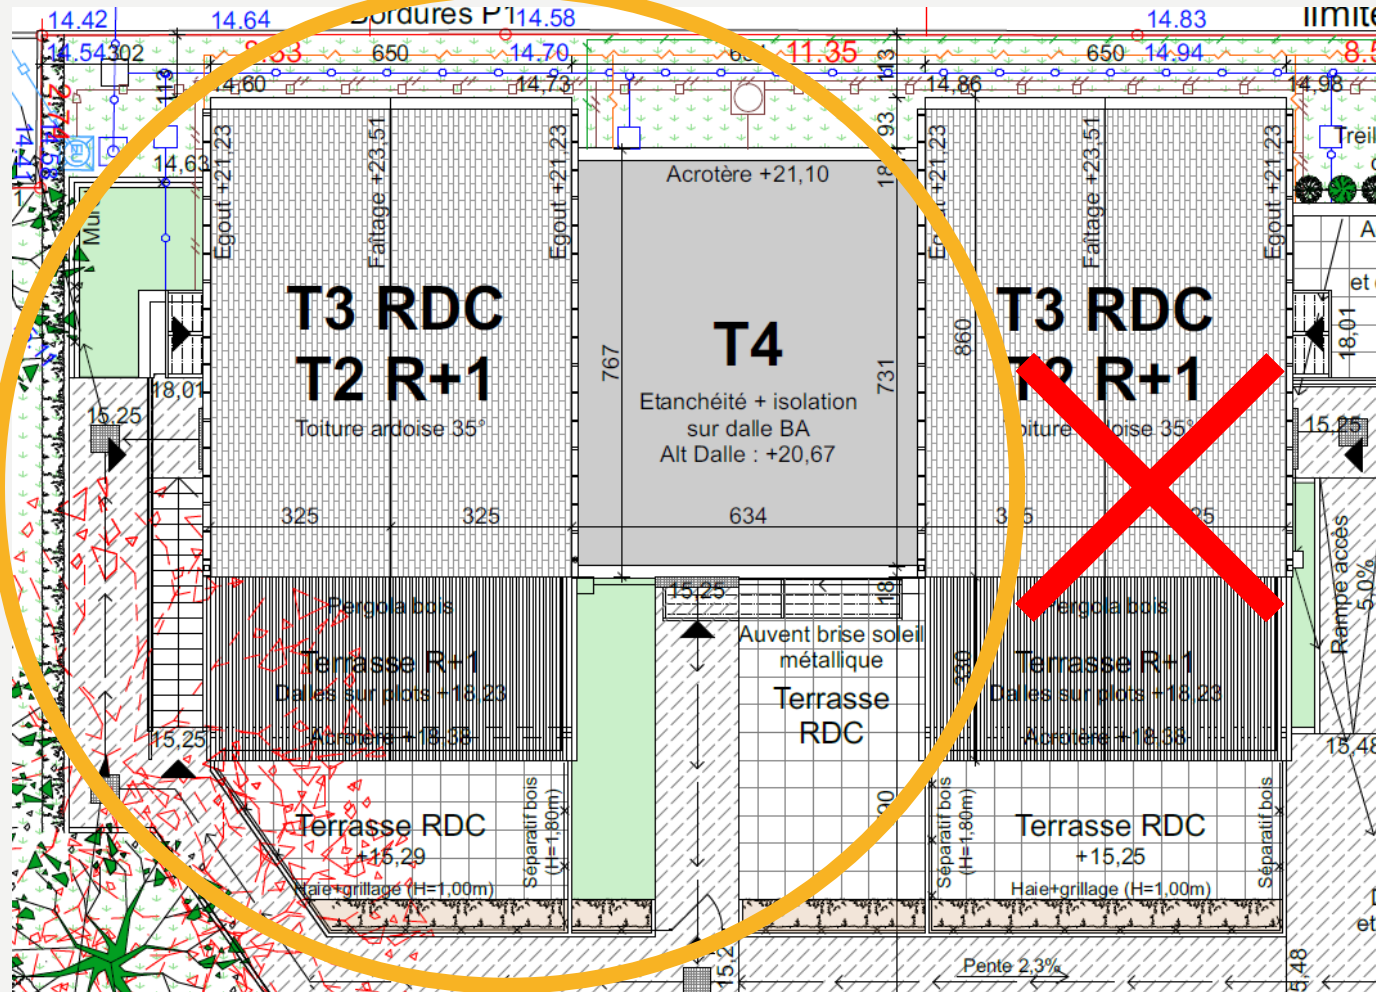


PRÉSENTATION DU PROJET THOANNIC

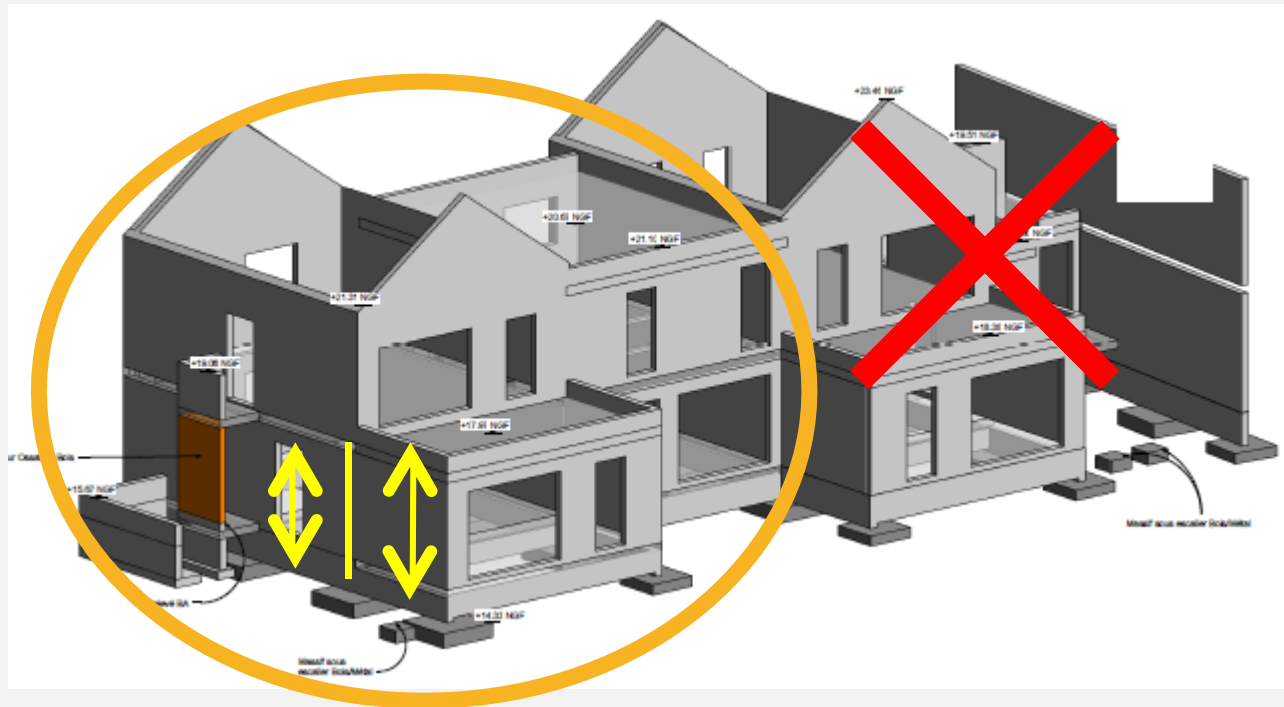

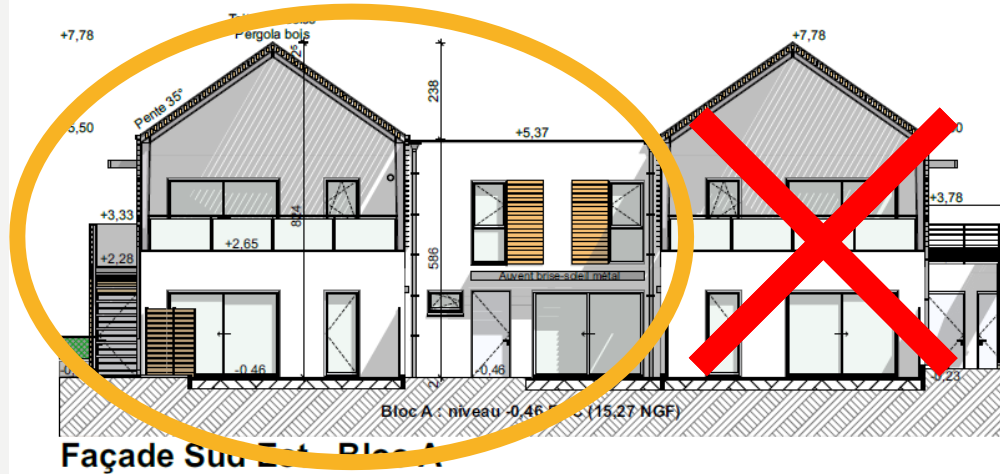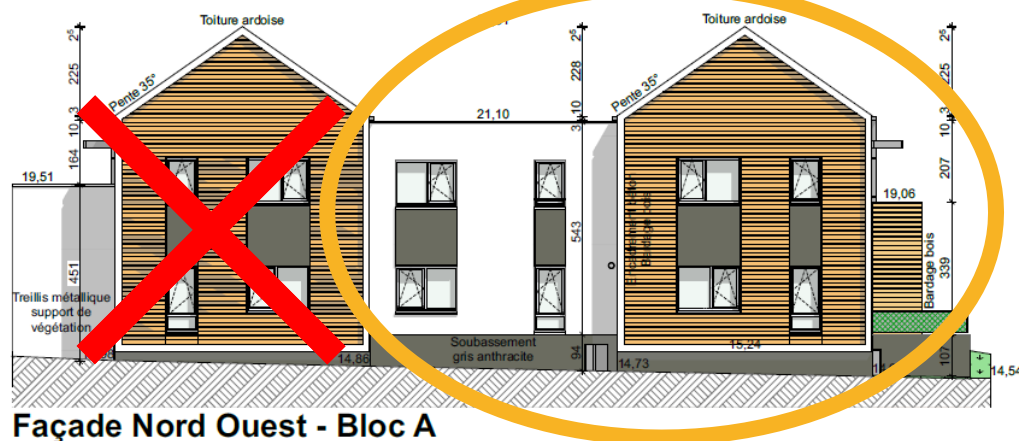

MADOC : PIÈCES GRAPHIQUES

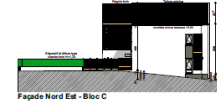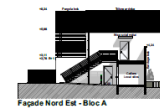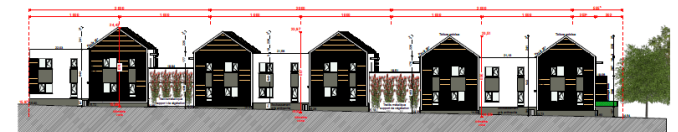

MADOC : PIÈCES ÉCRITES

Darys Habitat

11 rue Daubrée
44100 NANTES

Tel : 09.80.44.82.48 Email : arnaud.bodenan@daryshabitat.com



Construction de 13 logements collectifs

Rue du Tohannic -
56000 - VANNES

C.C.T.P.



MAÎTRE D'OEUVRE CAP ARCHITECTURE

45 rue de Telorn
29200 BREST
Tel : 02.98.33.25.40 Fax : 02.98.33.25.41 Email : info@caparchitecture.com



BUREAU D'ETUDES FLUIDES ATIS

72 Bd Gambetta
29200 BREST
Tel : 02.98.46.32.19 Email : atis@atis.bzh



BUREAU D'ETUDES STRUCTURES ESL

75 rue Jules Janin
29490 GUIPAVAS
Tel : 02.98.07.74.57 Email : contact@esl-29.com

MADOC :

REVIT TOHANNIC



Plans et CCTP TOHANNIC

Aide REVIT

Gabarit Revit pour TOHANNIC

Document à suivre

Fichiers Revit

Compris : menuiseries extérieures, pergola, escalier extérieur, cloison de distribution, ...)

Etiquettes de pièces, cartouches,...

MADOC :

REVIT TOHANNIC




Plans et CCTP TOHANNIC

Aide REVIT

Gabarit Revit pour TOHANNIC

Document à suivre

Fichiers Revit

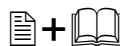

THOANNIC – CREATION ET EXPLOITATION D'UNE MAQUETTE NUMERIQUE

NOM _____ PRENOM _____

« Ce document est à compléter au cours de la séance par l'étudiant.
L'enseignant le complète en parallèle pour suivre la progression de l'étudiant.

Absence(s) : Séance 1 ☐ Séance 2 ☐ Séance 3 ☐ Séance 4 ☐ Séance 5 ☐ Séance 6 ☐ Séance 7 ☐
Remarques :



Le symbole  indique qu'un **Q&A** explicatif spécifique est disponible sur MADOC

Le symbole  indique que des explications figurent dans le manuel de survie REVIT

Le symbole  indique qu'il faut faire valider son travail par l'enseignant

Remarques éventuelles

REGLAGES PREALABLES, NIVEAUX ET QUADRILLAGES

Réaliser le travail préalable de repérage des niveaux

☐

Ouvrir le gabarit de MADOC

☐

Changer l'unité (cm)

☐

Sur une élévation **créer** les niveaux

☐

0 rdc, 1 étage, 2 **toiture** terrasse, fondation, plan de masse

Régler ces niveaux (EN BLEU) conformément aux plans

☐

Placer les principaux niveaux (EN NOIR 1) sur une élévation

☐

Arases inférieures :	Dalle de l'étage	Dalle de la toiture terrasse
Dalle du rdc :		
Arases supérieures :	Dalle de l'étage	Dalle de la toiture terrasse
Dalle du rdc :		
Faux plafond de l'étage		
Faitage		
Couvertine de la toiture terrasse		
Couvertine de la terrasse de l'étage		
Arase supérieure de voie de l'étage		
Arase supérieure de la cloison de l'escalier duplex		

Organiser les niveaux (bleu à droite, noir à gauche, pas trop éloignés, lisibles, triés...)

☐

Tracer le quadrillage au ou extérieur des murs

☐

Organiser le quadrillage (milieu de la page, pas trop grands...)

☐

Placer 4 coupes sur une vue en plan (2 longitudinales et 2 transversales)

☐

Régler partout l'échelle et l'affichage (1/50 ; niveau de détails élevé ; couleurs uniformes)

☐

TRAVAIL DEMANDÉ :

- 1) Monter la maquette numérique
- 2) Exploiter cette maquette :
 - Générer un dossier de plan
 - Générer une visite virtuelle

DOCUMENT À SUIVRE :

THOANNIC – CREATION ET EXPLOITATION D'UNE MAQUETTE NUMERIQUE

NOM _____ PRENOM _____

⚡ Ce document est à compléter au cours de la séance par l'étudiant.
L'enseignant le complète en parallèle pour suivre la progression de l'étudiant.

Absence(s) : Séance 1 ☐ Séance 2 ☐ Séance 3 ☐ Séance 4 ☐ Séance 5 ☐ Séance 6 ☐ Séance 7 ☐

Remarques : _____



Le symbole  indique qu'un pdf explicatif spécifique est disponible sur MADOC

Le symbole  indique que des explications figurent dans le manuel de survie REVIT

Le symbole  indique qu'il faut faire valider son travail par l'enseignant

REGLAGES PREALABLES, NIVEAUX ET QUADRILLAGES  

Réaliser le travail préalable de repérage des niveaux ☐

Ouvrir le gabarit de MADOC ☐

Changer l'unité (cm) ☐

Dans l'arborescence renommer les niveaux
0 rdc, 1 étage, 2 toiture terrasse, fondation, plan de masse ☐

Régler ces niveaux (EN BLEU) conformément aux plans ☐

Placer les principaux niveaux (EN NOIR !) sur une élévation ☐

Arases inférieures :		☐
Dalle du rdc	Dalle de l'étage	Dalle de la toiture terrasse
Arases supérieures :		☐
Dalle du rdc	Dalle de l'étage	Dalle de la toiture terrasse
Faux plafond de l'étage		☐
Faitage		☐
Couvertine de la toiture terrasse		☐
Couvertine de la terrasse de l'étage		☐
Arase supérieure de voie de l'étage		☐
Arase supérieure de la cloison de l'escalier duplex		☐

Organiser les niveaux (bleu à droite, noir à gauche, pas trop éloignés, lisibles, triés...) ☐

Tracer le quadrillage au nu extérieur des murs ☐

Organiser le quadrillage (milieu de la page, pas trop grands...) ☐

Placer 4 coupes (stratégiquement... 2 verticales et 2 horizontales) ☐

Régler partout l'échelle et l'affichage (1/50, niveau de détails élevé ; couleurs uniformes) ☐

⚡ Ce document est à compléter au cours de la séance par l'étudiant.
L'enseignant le complète en parallèle pour suivre la progression de l'étudiant.

Le symbole  indique qu'un pdf explicatif spécifique est disponible sur MADOC

Le symbole  indique que des explications figurent dans le manuel de survie REVIT

Le symbole  indique qu'il faut faire valider son travail par l'enseignant

TOITURE

Dupliquer le toit de base pour composer la toiture

Tracer la toiture (régler l'inclinaison, la position à l'arase supérieure des voiles)


Attacher les pignons à la toiture



POINT D'ARRET  : Validation de l'enseignant




ÉLÉMENTS DANS LE GABARIT :

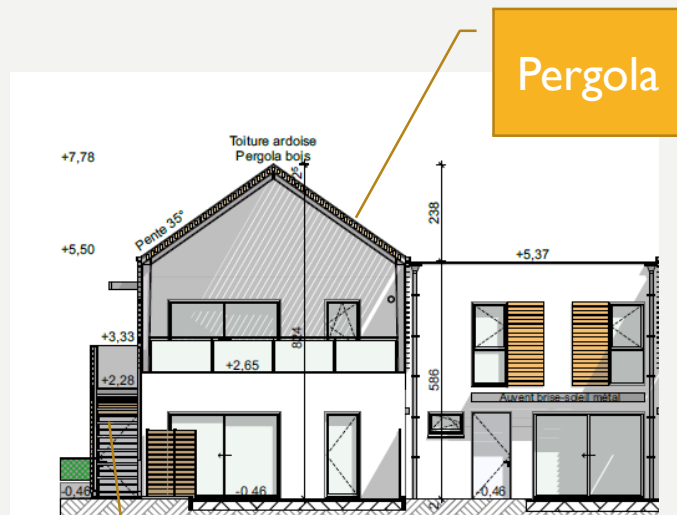

Pergola

Escalier
extérieur

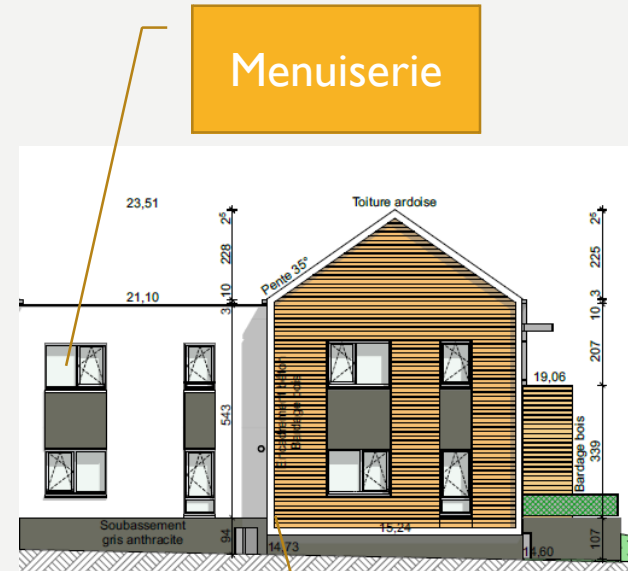


Menuiserie

Bandeau
béton

Dans l'arborescence renommer les niveaux

0 rdc, 1 étage, 2 toiture terrasse, fondation, plan de masse

Régler ces niveaux (EN BLEU) conformément aux plans

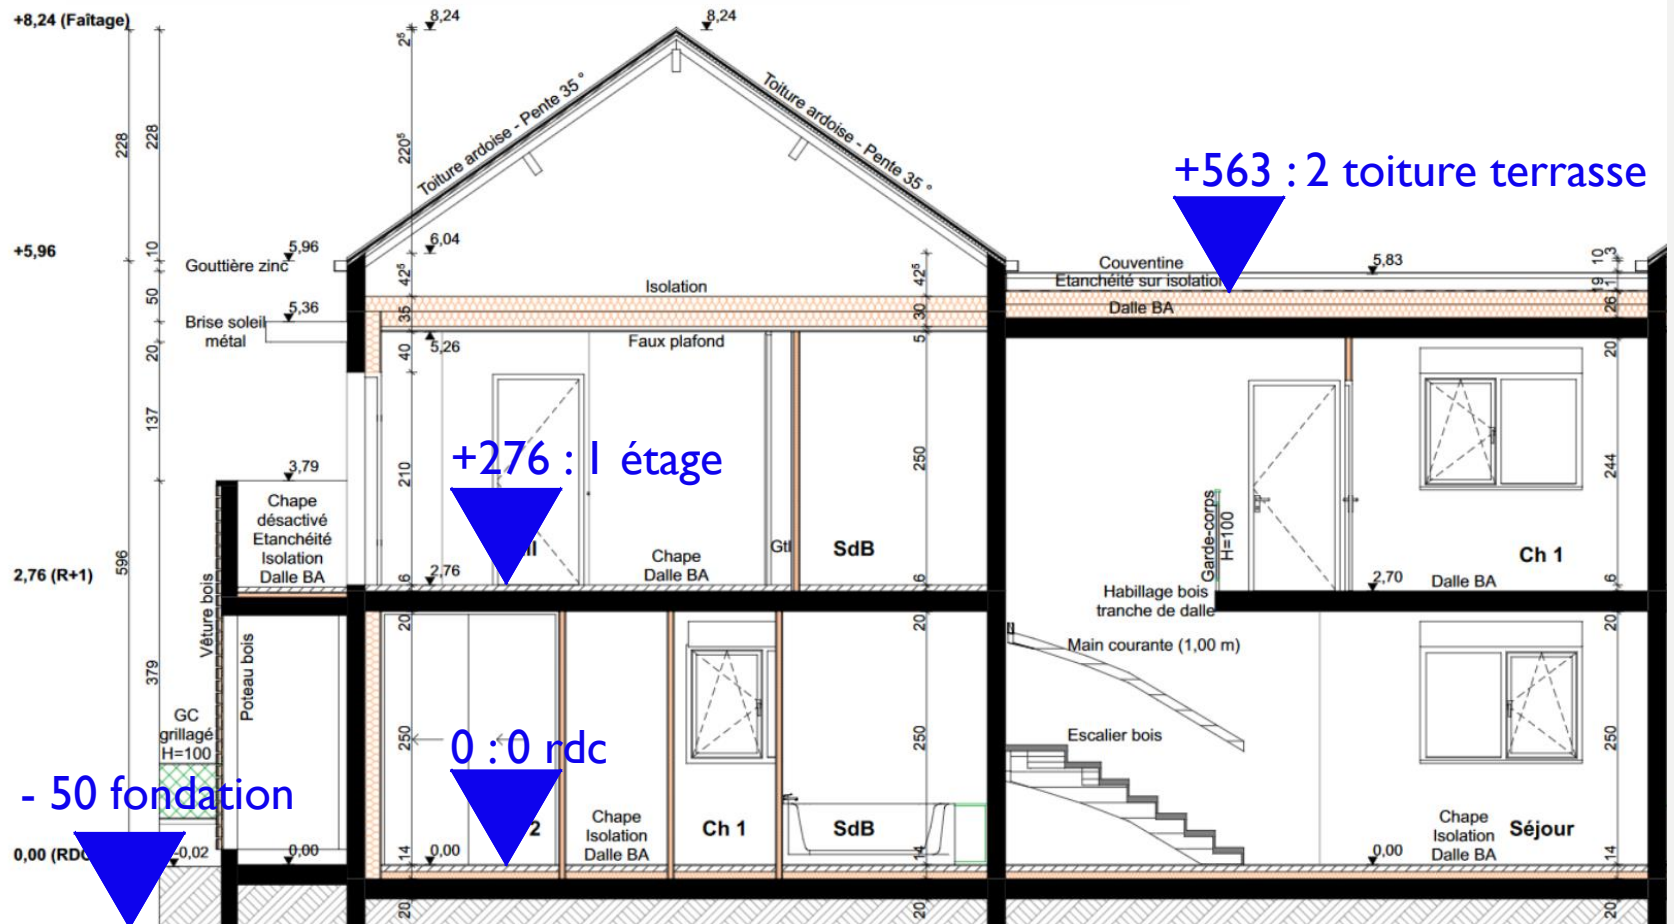

Placer les principaux niveaux (EN NOIR !) sur une élévation

Arases inférieures :

Dalle du rdc

Dalle de l'étage

Dalle de la toiture terrasse

Arases supérieures :

Dalle du rdc

Dalle de l'étage

Dalle de la toiture terrasse

Faux plafond de l'étage

Faitage

Couvertine de la toiture terrasse

Couvertine de la terrasse de l'étage


Arase supérieure de voile de l'étage

Arase supérieure de la cloison de l'escalier duplex



+520
Al dalle
de la
toiture
terrasse

+540
AS dalle
de la
toiture
terrasse

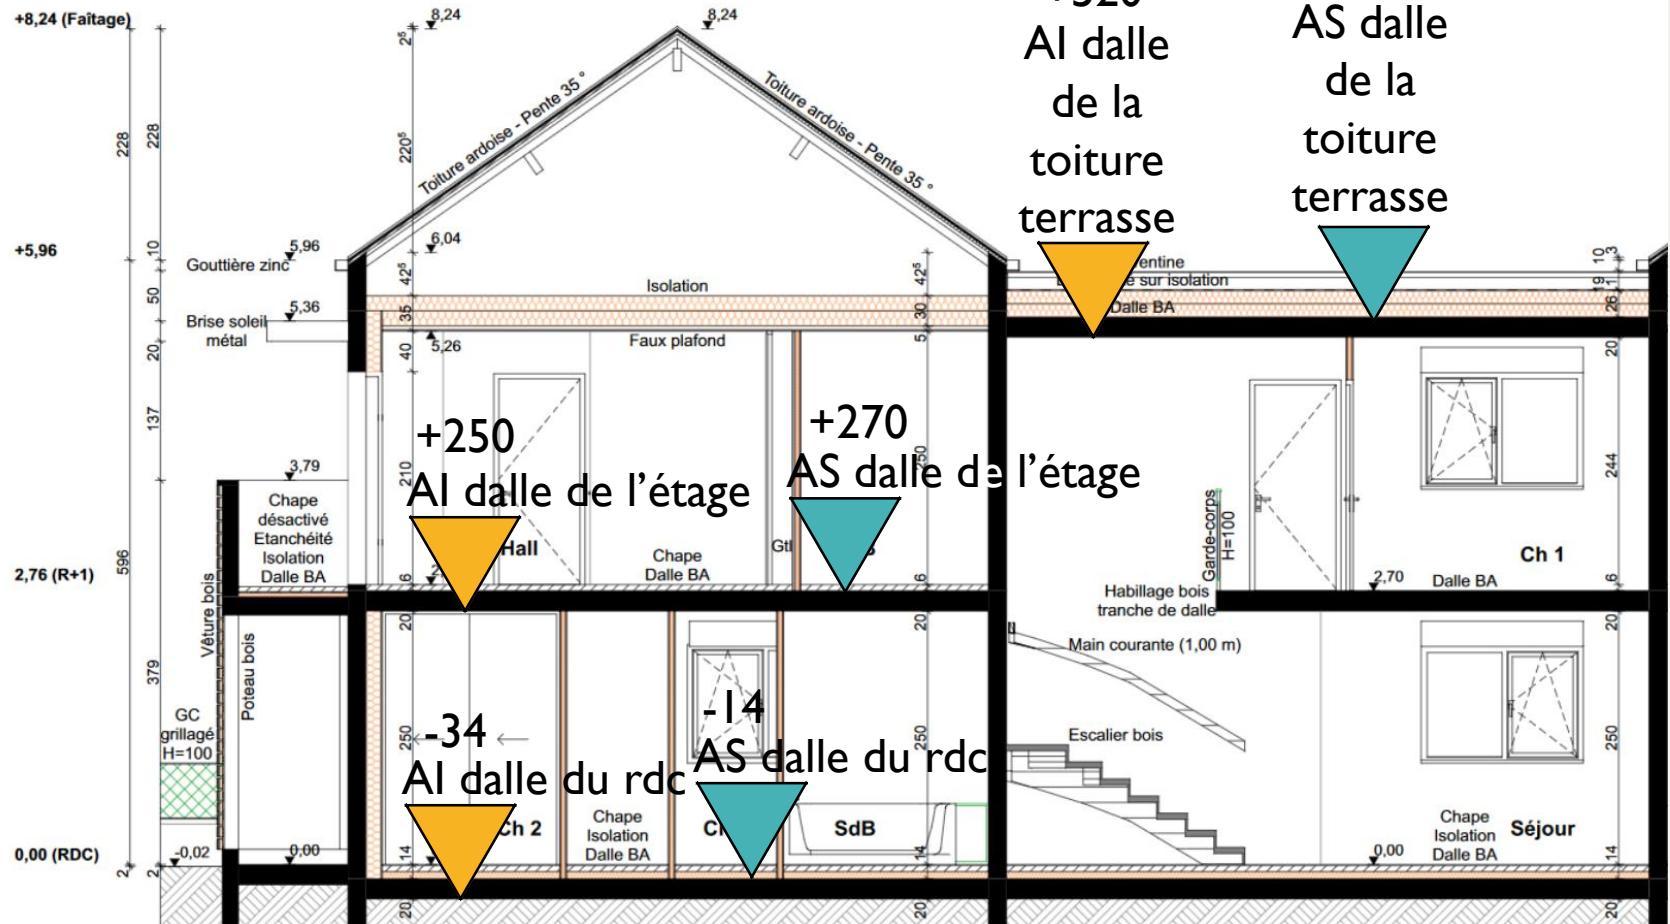

Placer les principaux niveaux (EN NOIR !) sur une élévation

Arases inférieures :

Dalle du rdc

Dalle de l'étage

Dalle de la toiture terrasse

Arases supérieures :

Dalle du rdc

Dalle de l'étage

Dalle de la toiture terrasse

Faux plafond de l'étage

Faitage

Couvertine de la toiture terrasse

Couvertine de la terrasse de l'étage

Arase supérieure de voile de l'étage

Arase supérieure de la cloison de l'escalier duplex


+824

Faitage

 +583

Couvertine

de la
toiture
terrasse

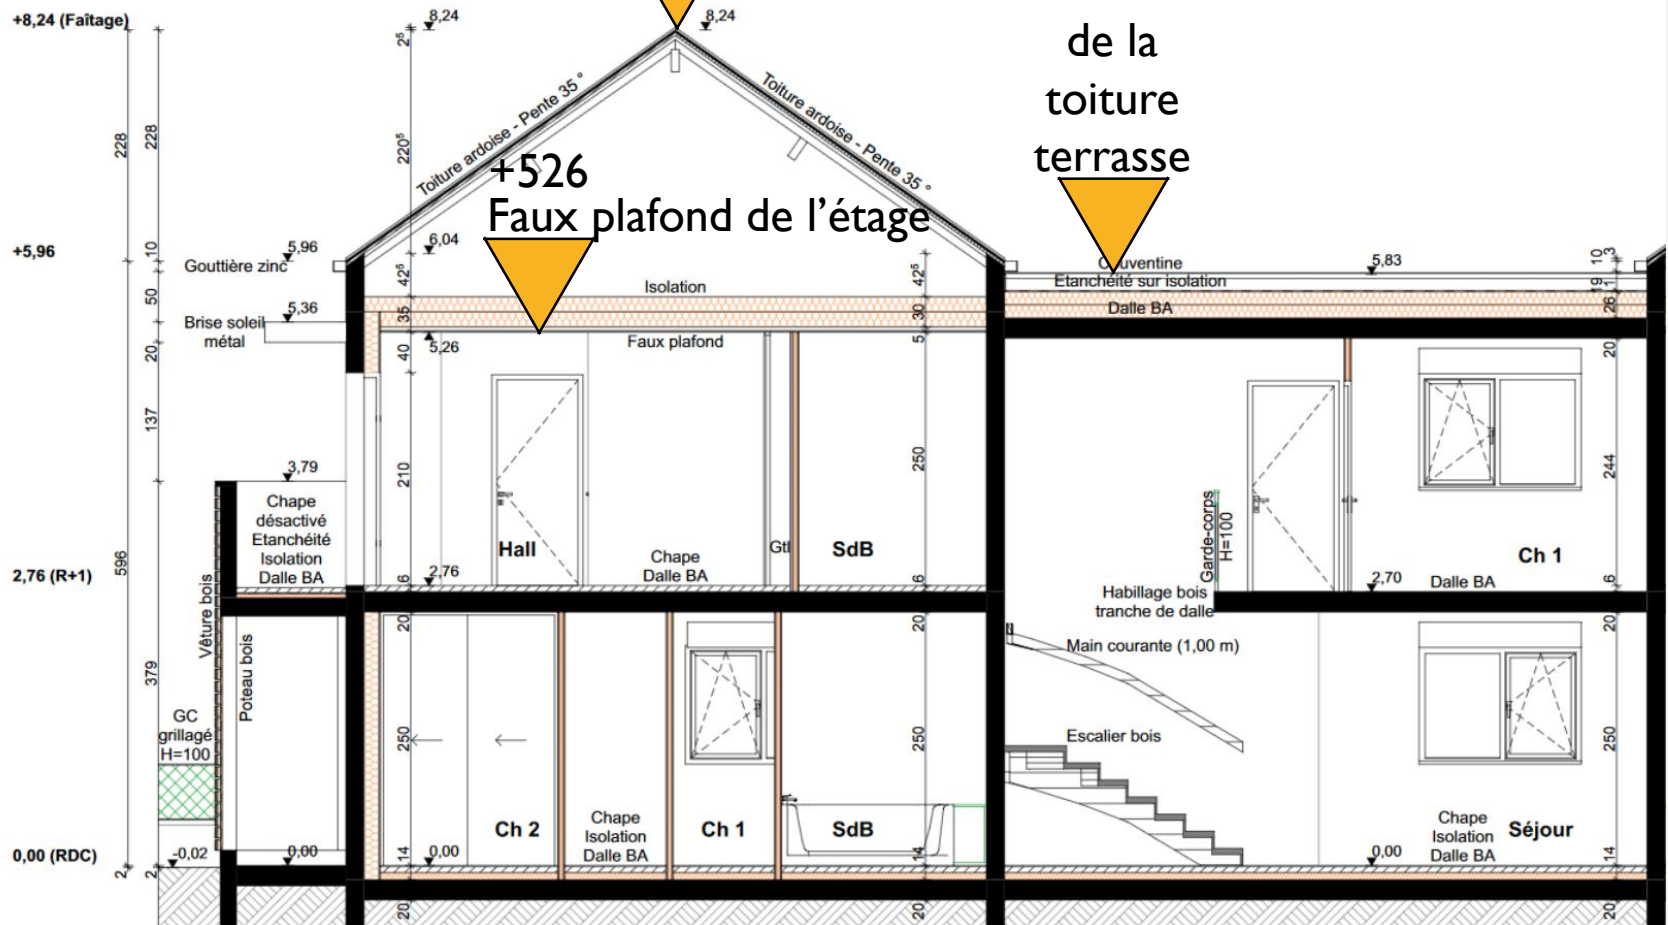

Placer les principaux niveaux (EN NOIR !) sur une élévation

Arases inférieures :

Dalle du rdc

Dalle de l'étage

Dalle de la toiture terrasse

Arases supérieures :

Dalle du rdc

Dalle de l'étage

Dalle de la toiture terrasse

Faux plafond de l'étage

Faitage

Couvertine de la toiture terrasse

Couvertine de la terrasse de l'étage


Arase supérieure de voile de l'étage

Arase supérieure de la cloison de l'escalier duplex




+3.11

Couvertine de la
terrasse de
l'étage

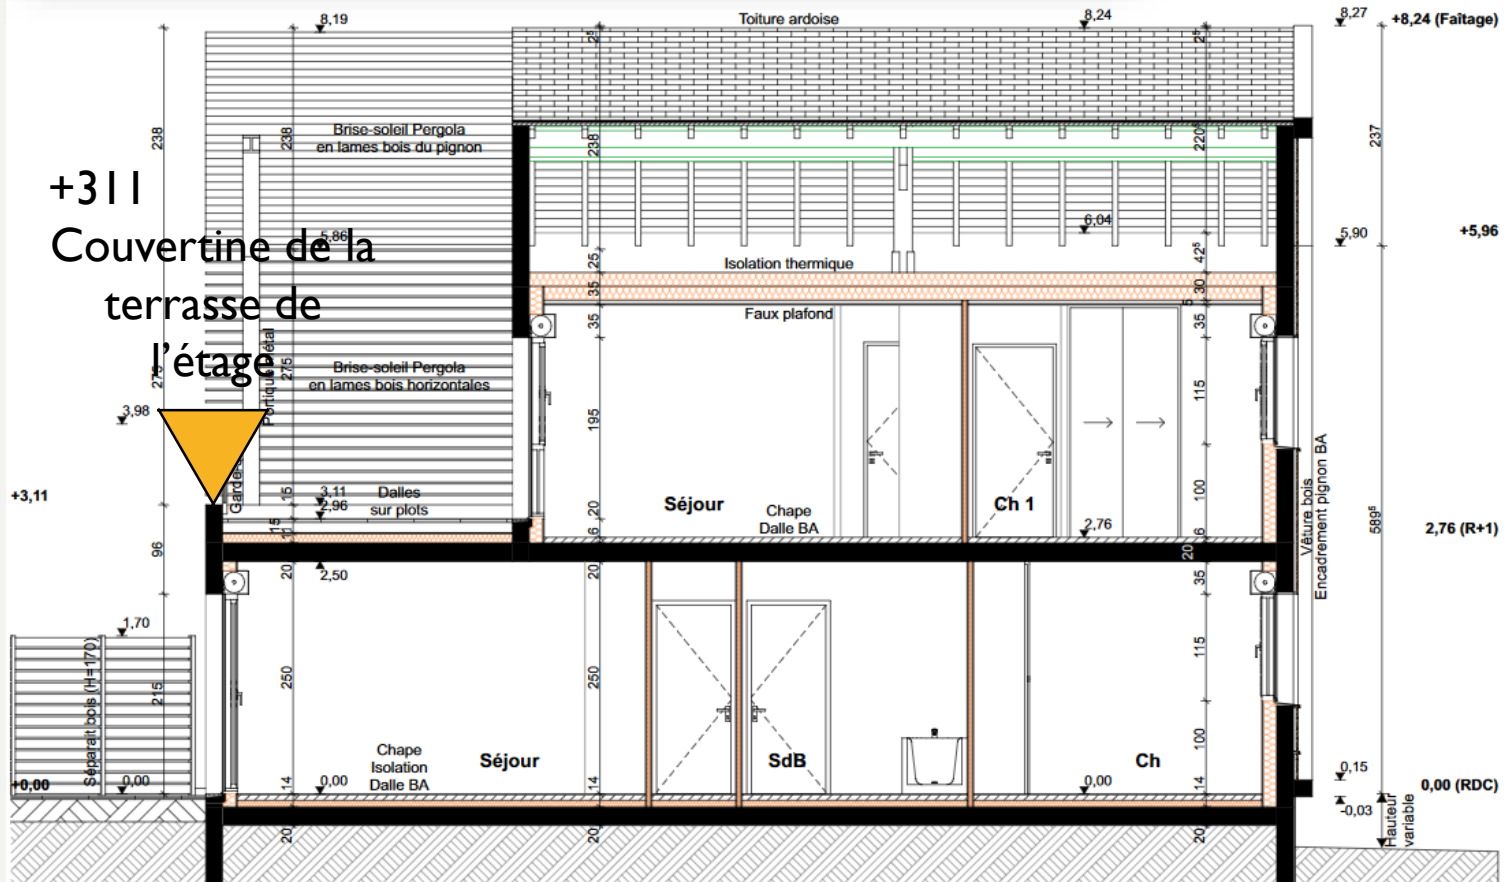

Placer les principaux niveaux (EN NOIR !) sur une élévation

Arases inférieures :			☐
Dalle du rdc	Dalle de l'étage	Dalle de la toiture terrasse	
Arases supérieures :			☐
Dalle du rdc	Dalle de l'étage	Dalle de la toiture terrasse	
Faux plafond de l'étage			☐
Faitage			☐
Couvertine de la toiture terrasse			☐
Couvertine de la terrasse de l'étage			☐
Arase supérieure de voile de l'étage			☐
Arase supérieure de la cloison de l'escalier duplex			☐

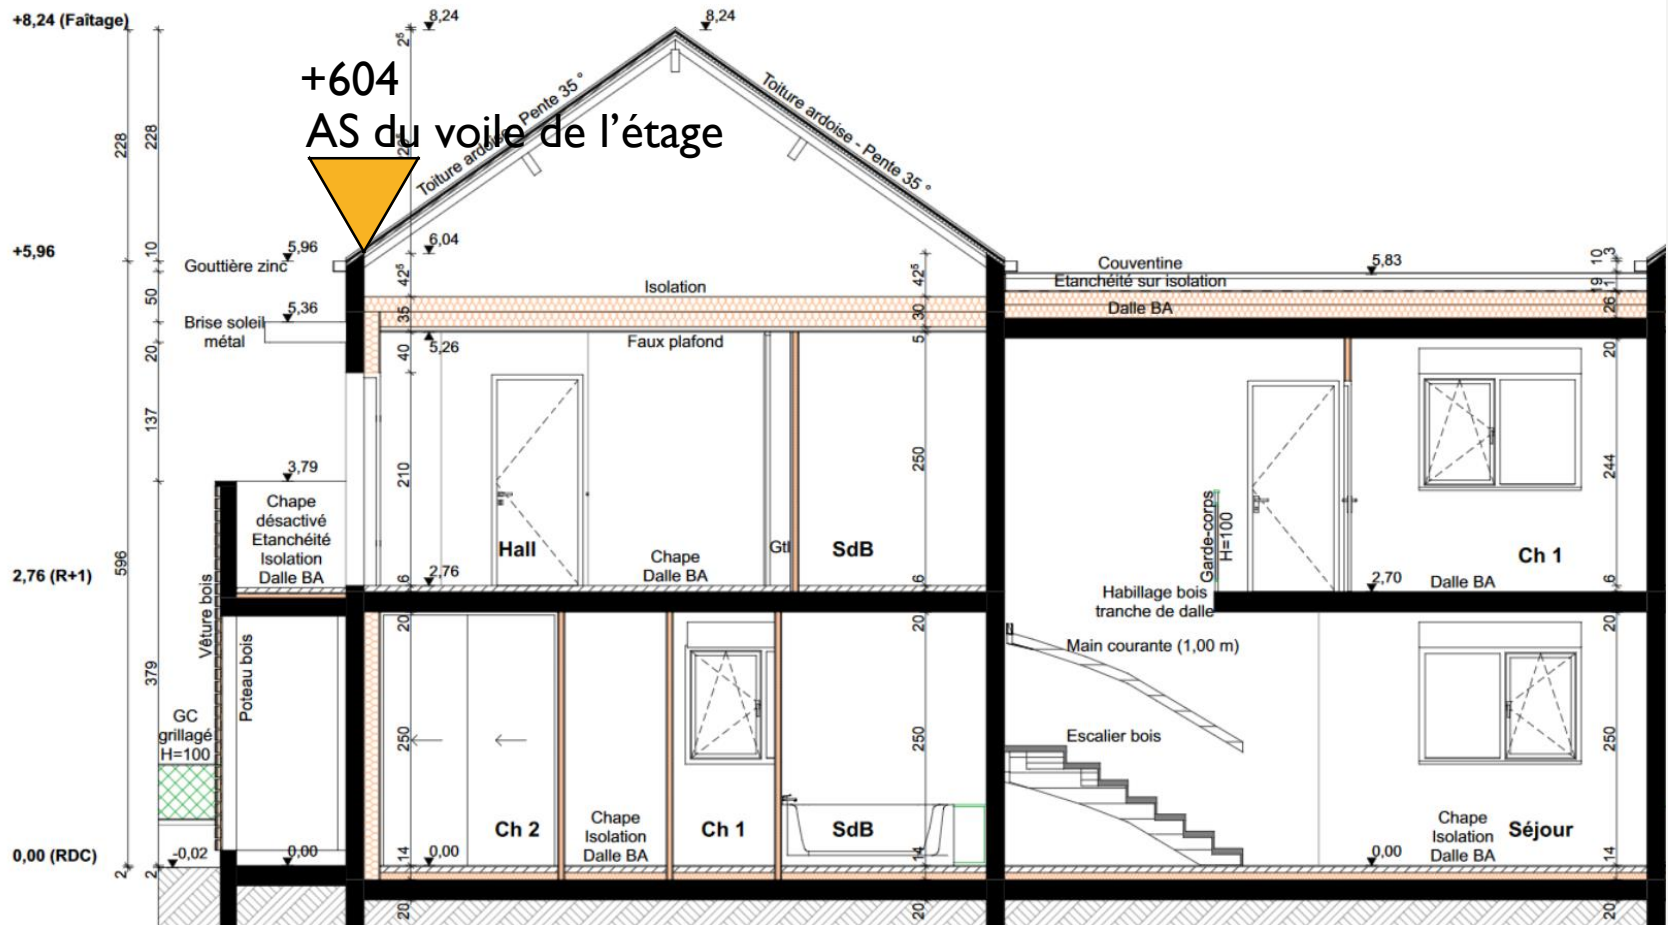

Placer les principaux niveaux (EN NOIR !) sur une élévation

Arases inférieures :

Dalle du rdc

Dalle de l'étage

Dalle de la toiture terrasse

Arases supérieures :

Dalle du rdc

Dalle de l'étage

Dalle de la toiture terrasse

Faux plafond de l'étage


Faitage

Couvertine de la toiture terrasse

Couvertine de la terrasse de l'étage


Arase supérieure de voile de l'étage

Arase supérieure de la cloison de l'escalier duplex

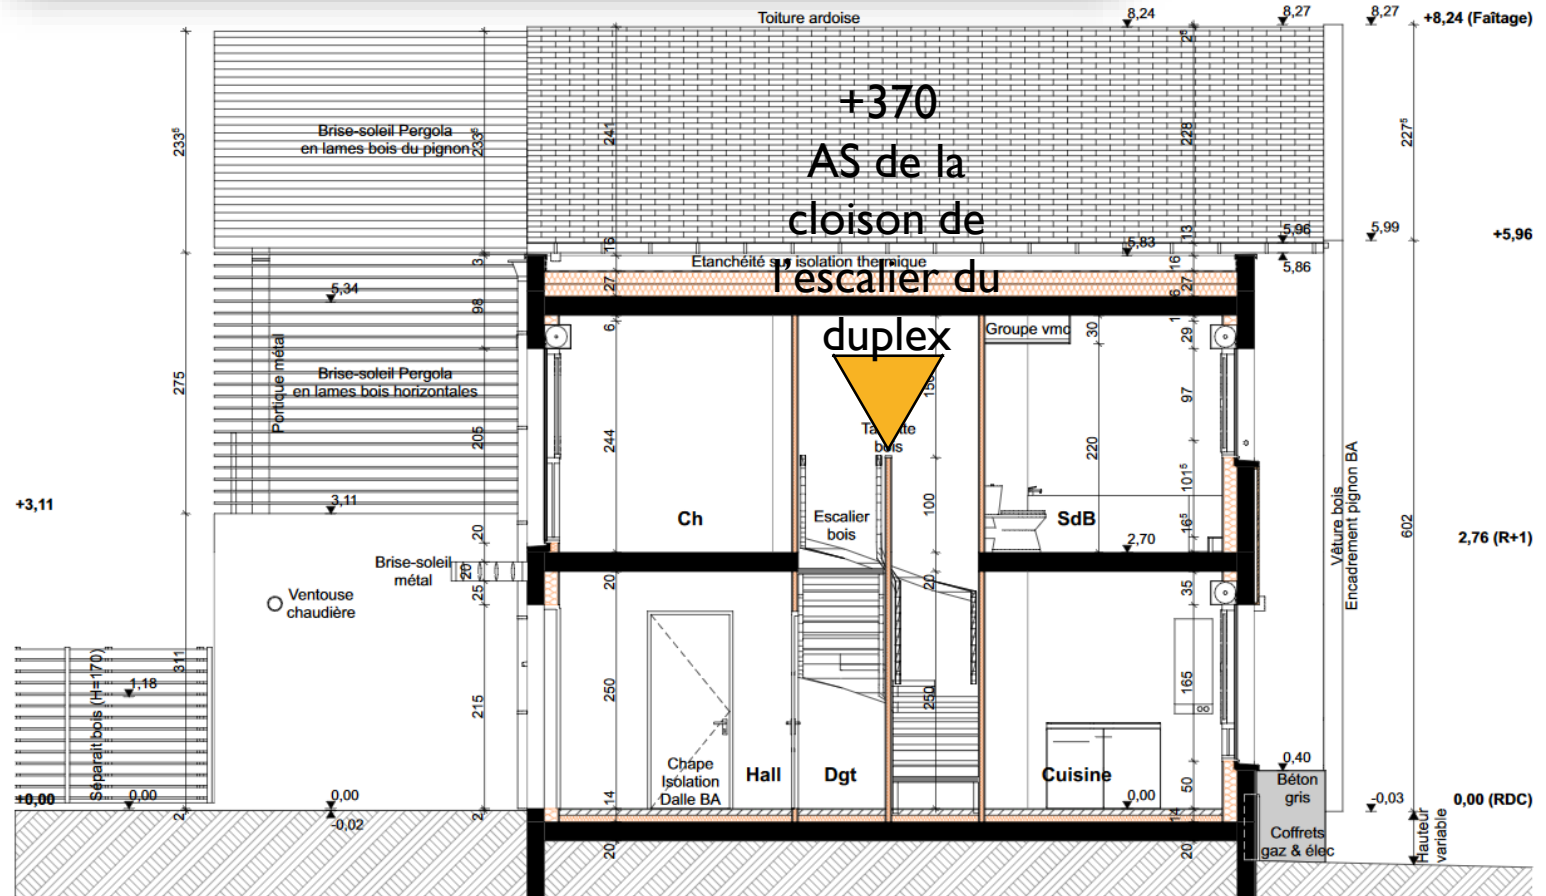


QUADRILLAGE :

Tracer le
quadrillage
au nu
extérieur
des murs

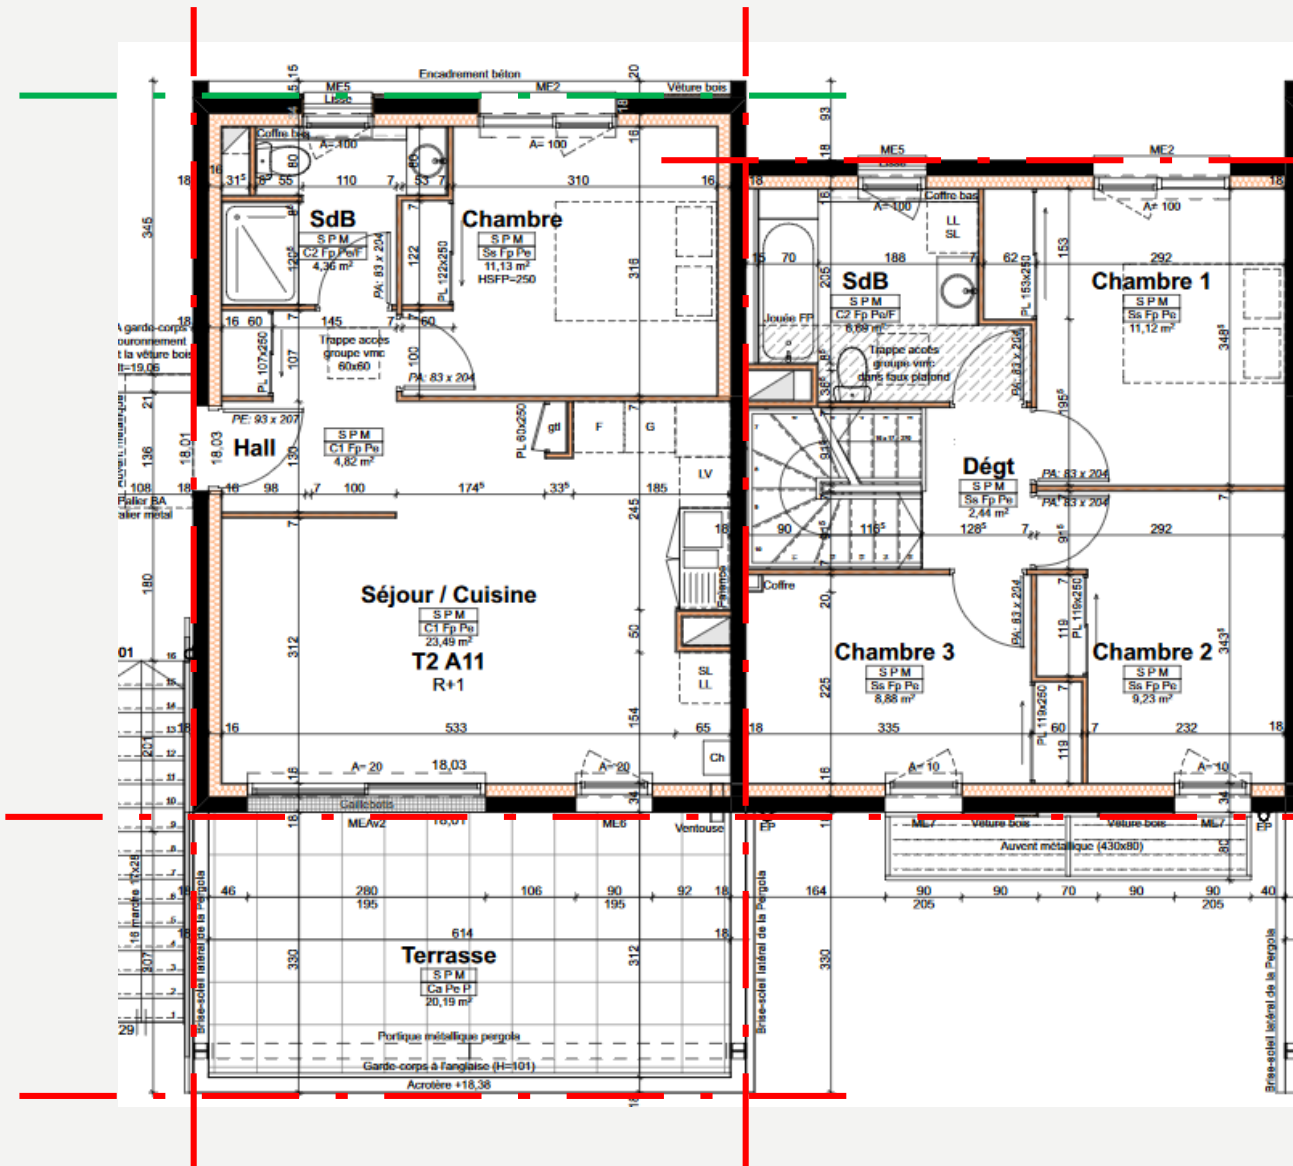

BANDEAU BÉTON

Le bandeau béton sera dessiné ultérieurement !
Dans notre maquette ce n'est pas un « mur »

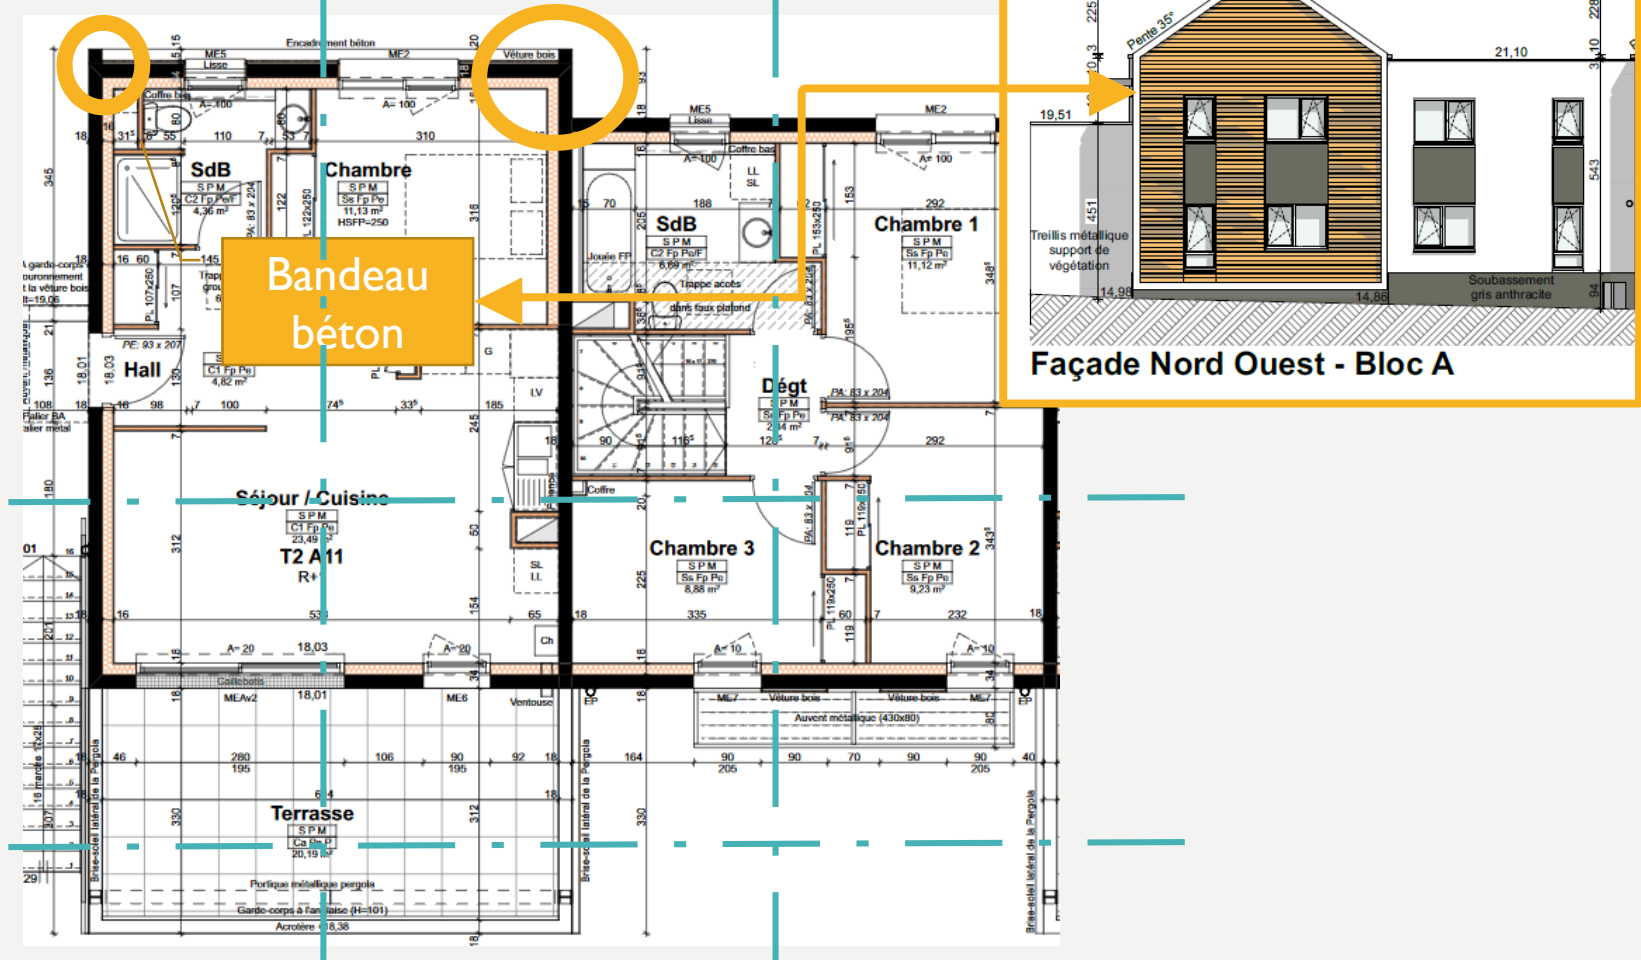

« MURS » :

TONNOM voile ba doublé

Voile béton + doublage

Ici aussi !!!
Car on ne représente pas tout le bloc A

TONNOM voile ba


Voile béton

Gaine technique


TONNOM gaine technique

Cloison de distribution

TONNOM cloison de distribution

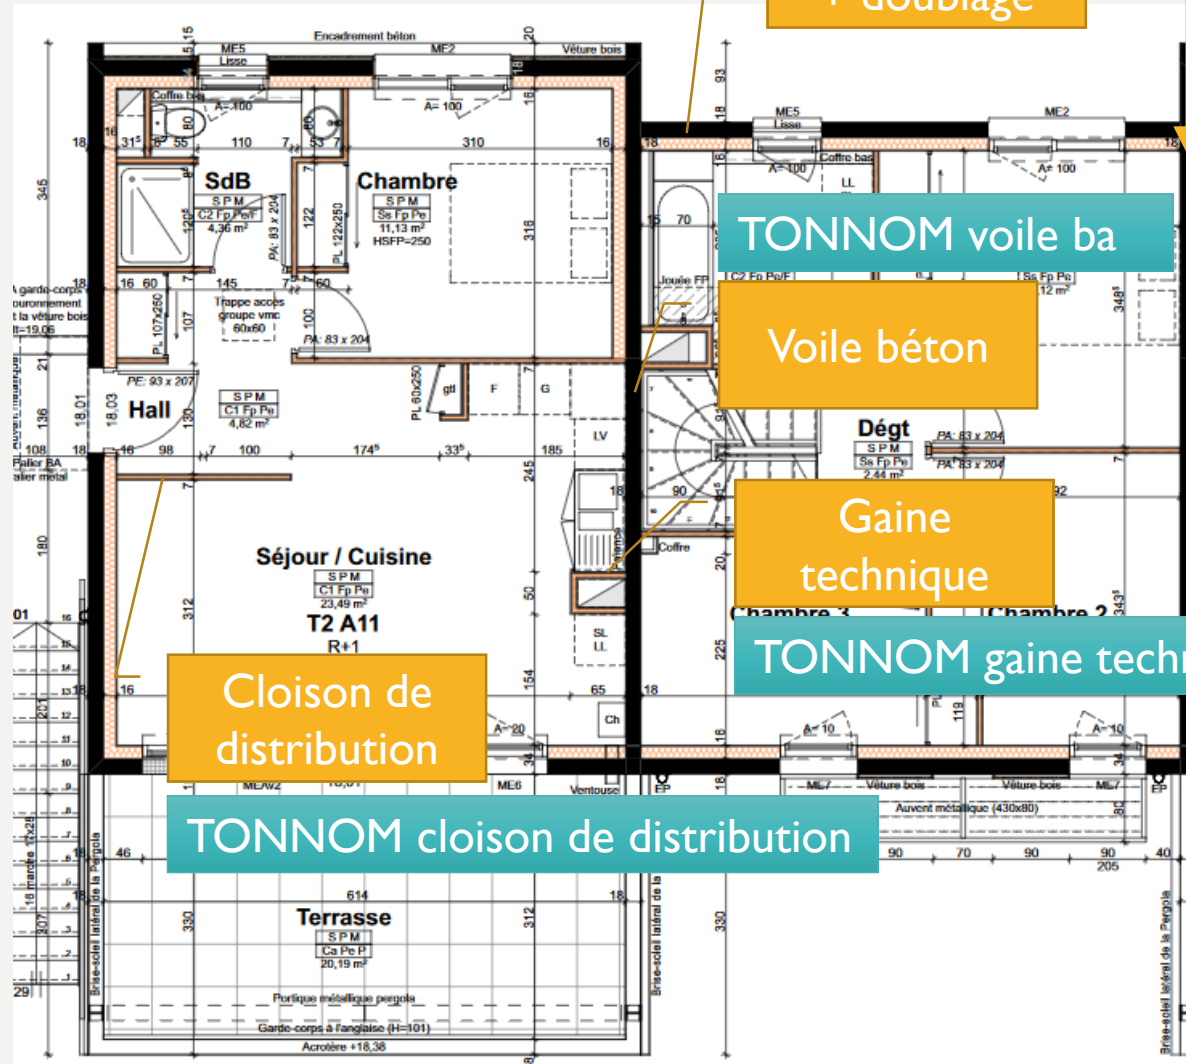


ATTENTION :

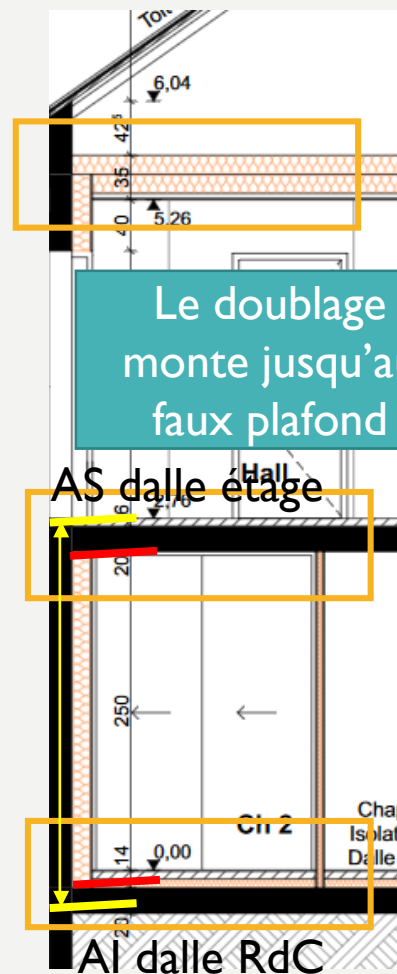

Le doublage monte jusqu'au faux plafond


AS dalle étage

Al dalle RdC

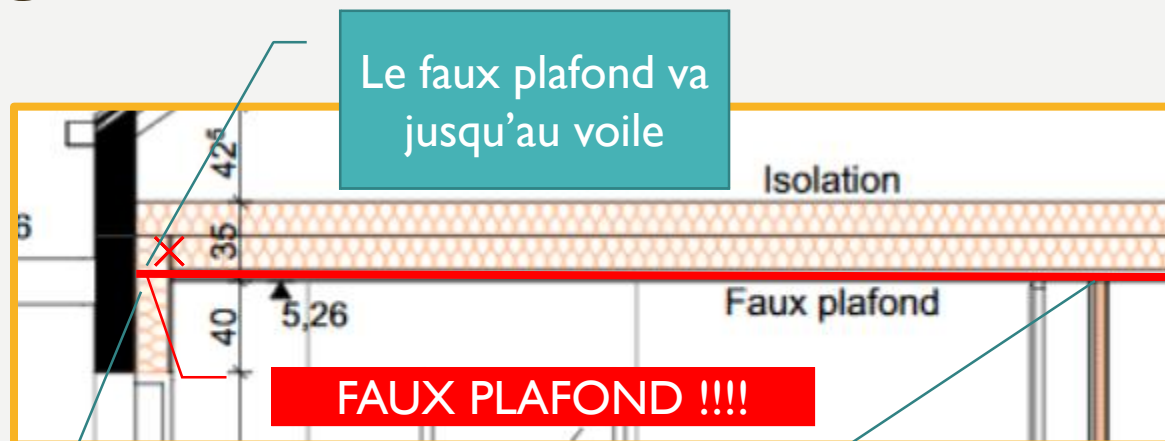

Le faux plafond va jusqu'au voile


FAUX PLAFOND !!!!

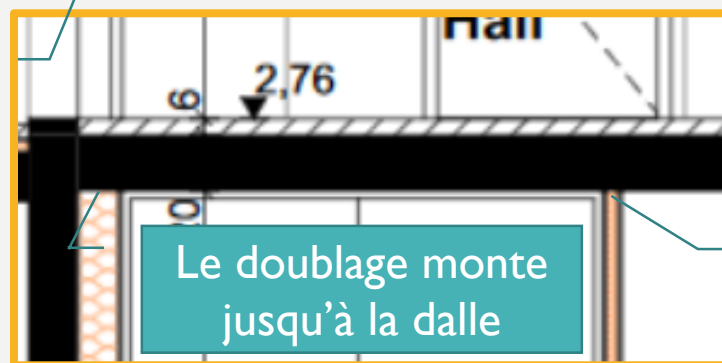

Le doublage monte jusqu'à la dalle

La cloison monte jusqu'au faux plafond

La cloison monte jusqu'à la dalle

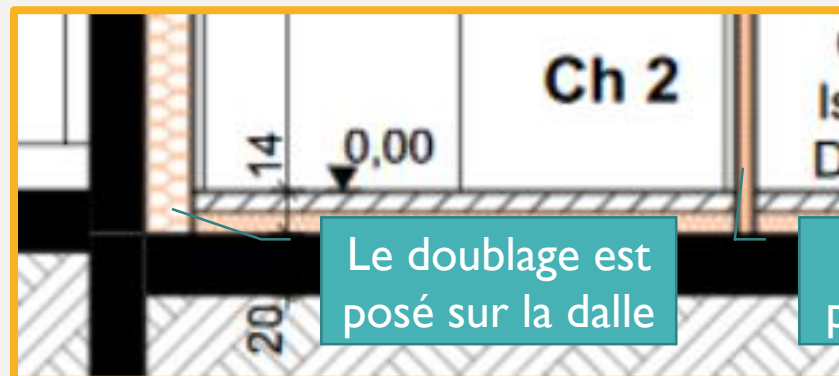

Le doublage est posé sur la dalle

La cloison est posée sur la dalle

