


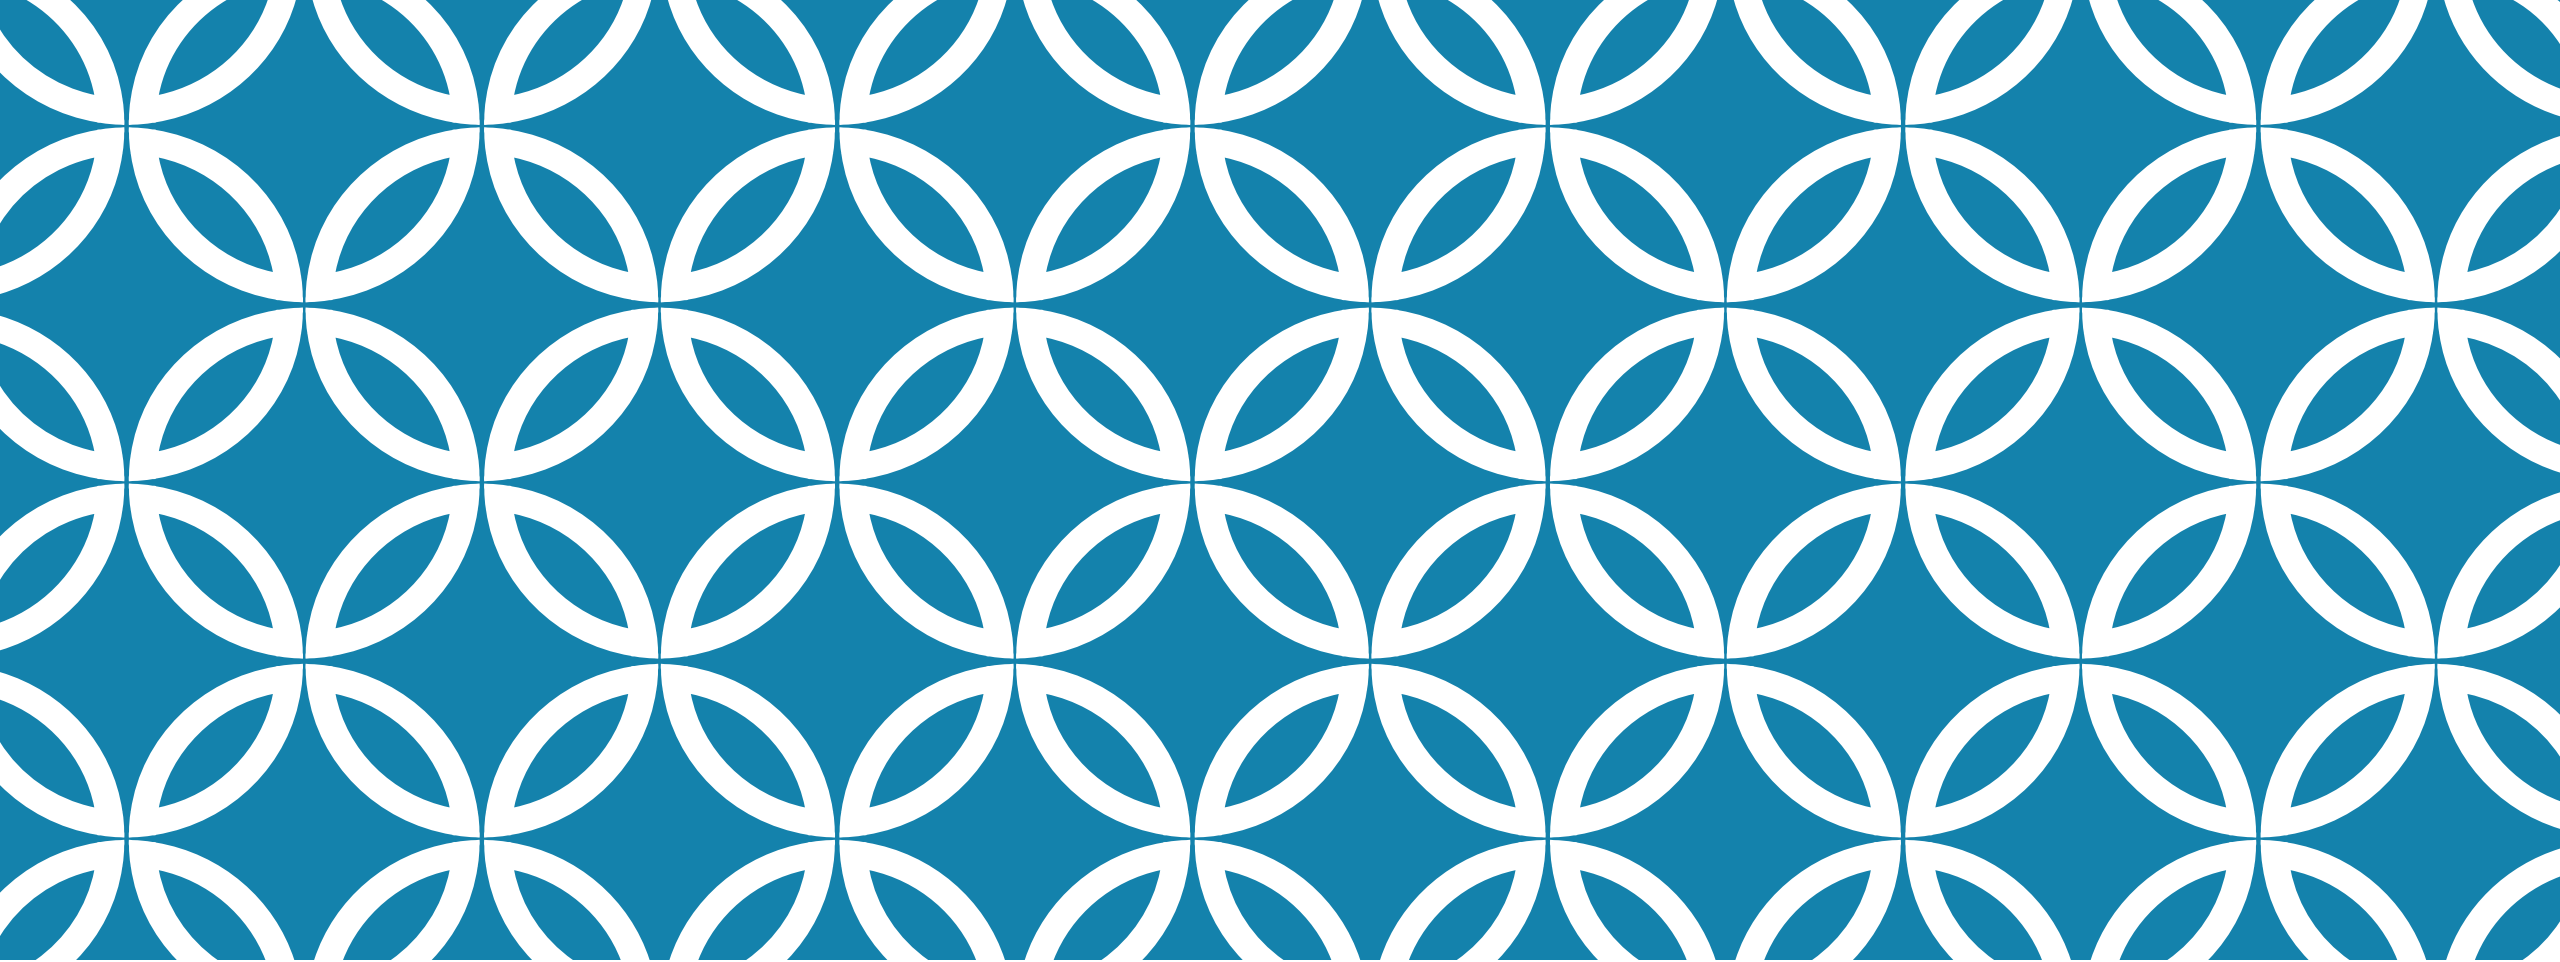

PROJET D'AMÉNAGEMENT DE BÂTIMENT

SAE 2.1

SAE 2.1 : PROJET D'AMÉNAGEMENT DE BÂTIMENT

COMPÉTENCE CIBLÉE :

Représenter des solutions techniques de tout ou partie d'un projet de bâtiment.

APPRENTISSAGES CRITIQUES :

Décrire les différentes technologies des bâtiments

Analyser des plans et des détails techniques

Produire des plans, coupes, détails techniques, schémas, en respectant les normes de dessin

ESPACE SIX CROIX : BÂTIMENTS À USAGE D'ACTIVITÉS ARTISANALES



PRÉSENTATION DU PROJET

Il s'agit d'un programme de 3 bâtiments à usage commercial, artisanal ou de stockage, construits à Donges. Les bâtiments sont livrés sans aménagements intérieurs et c'est à l'acquéreur d'effectuer les travaux complémentaires.

Les cellules se composent généralement de 2 volumes : un grand volume avec une hauteur sous plafond importante, situé à l'arrière pour les activités artisanales et de stockage, et un petit volume réservé à l'accueil donnant sur la façade principale, présentant un étage pouvant accueillir des bureaux, une salle de réunion, ou des vestiaires.


SITUATION




3 BÂTIMENTS À USAGE D'ACTIVITÉS ARTISANALES




BÂTIMENT B

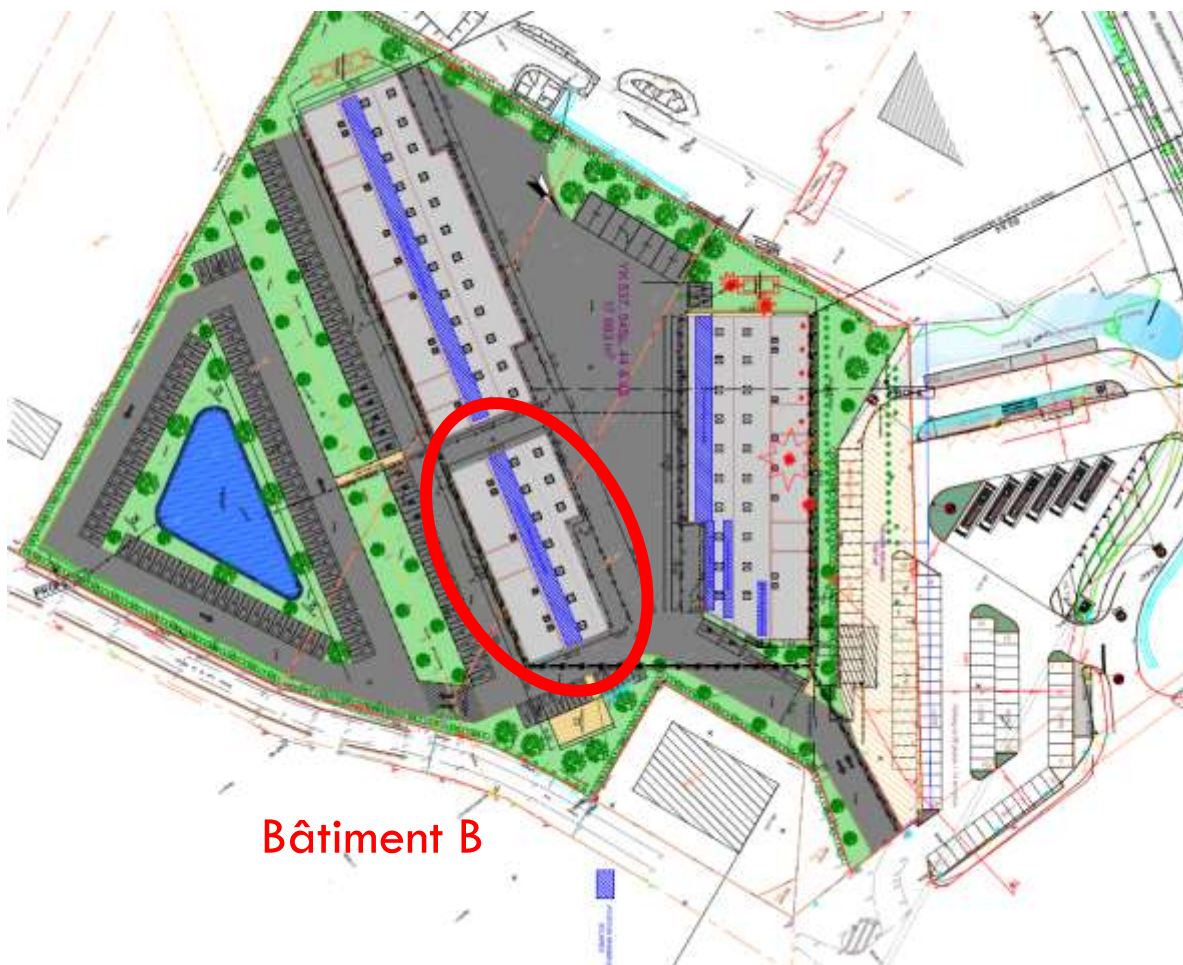

FAÇADES

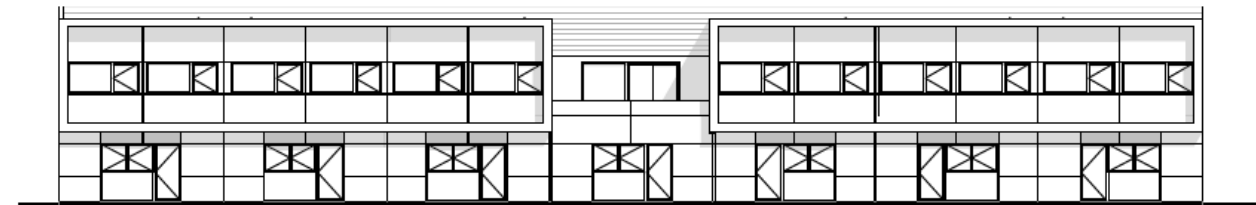


Façade EST 1:200

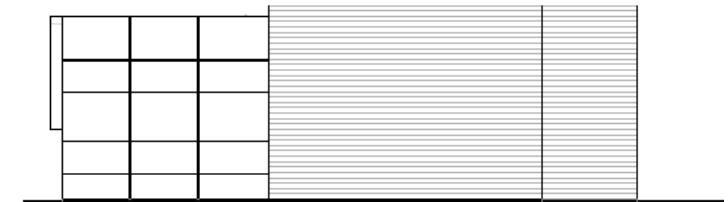

Façade NORD 1:200




Façade OUEST 1:200

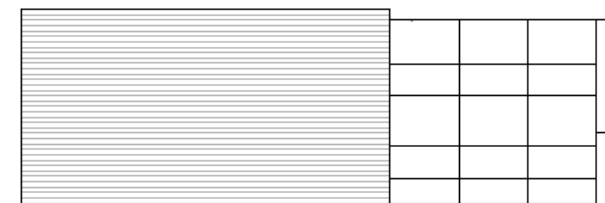

Façade SUD 1:200


VUES EN PLAN : 3 TYPES DE CELLULES

Cellule B7

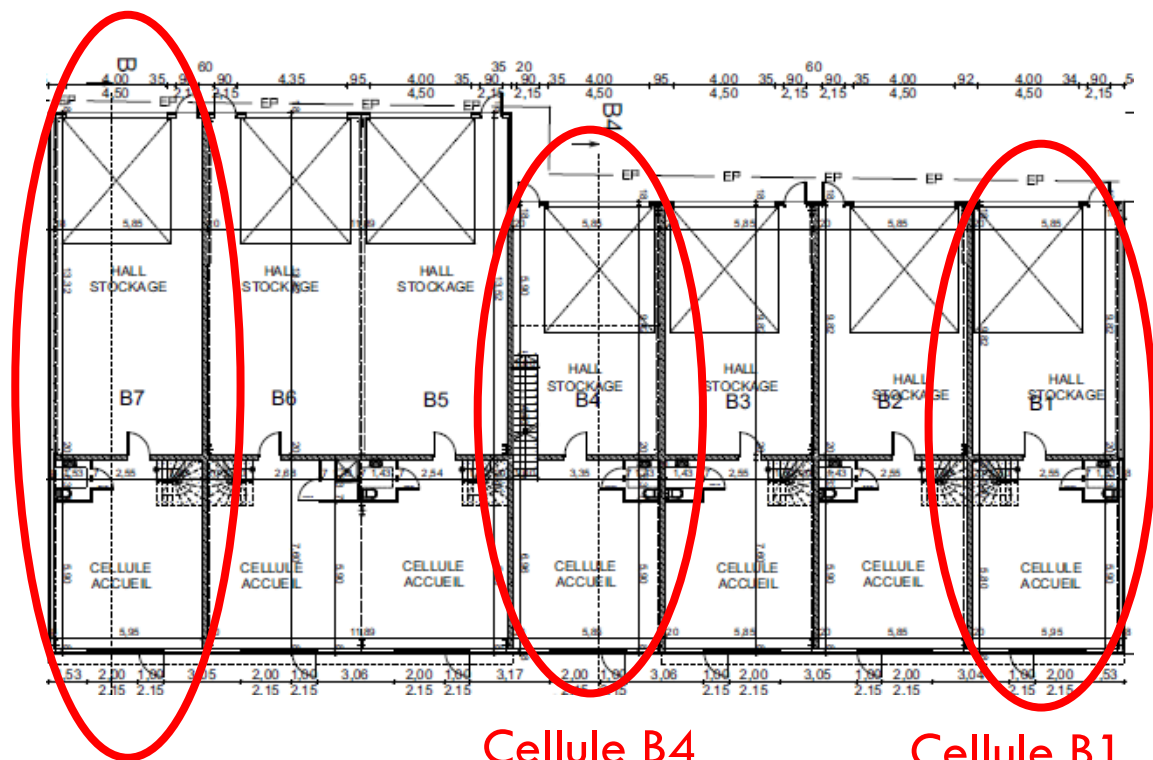


Cellule B4

Cellule B1

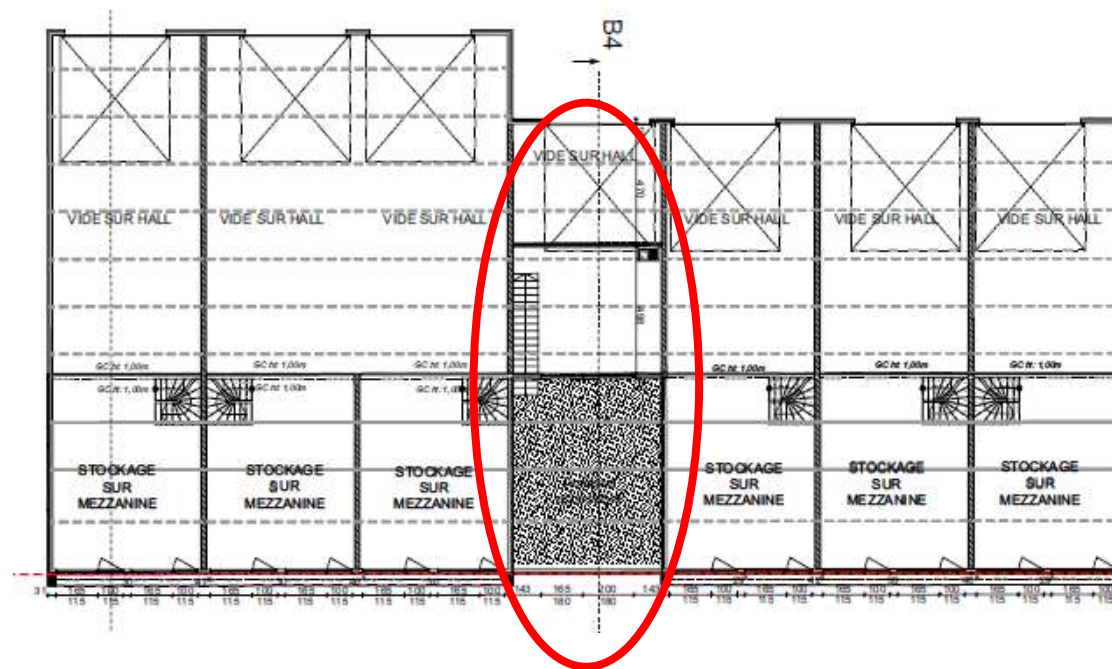


Cellule B4



VUES EN PLAN : CELLULE ETUDIÉE

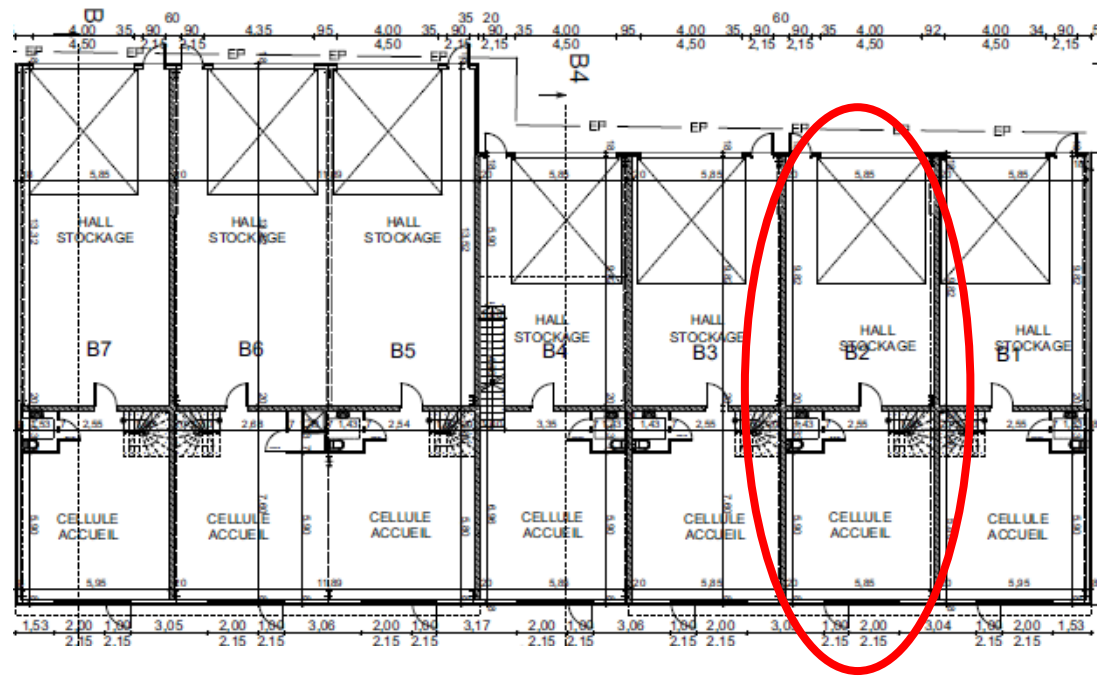

Cellule B2


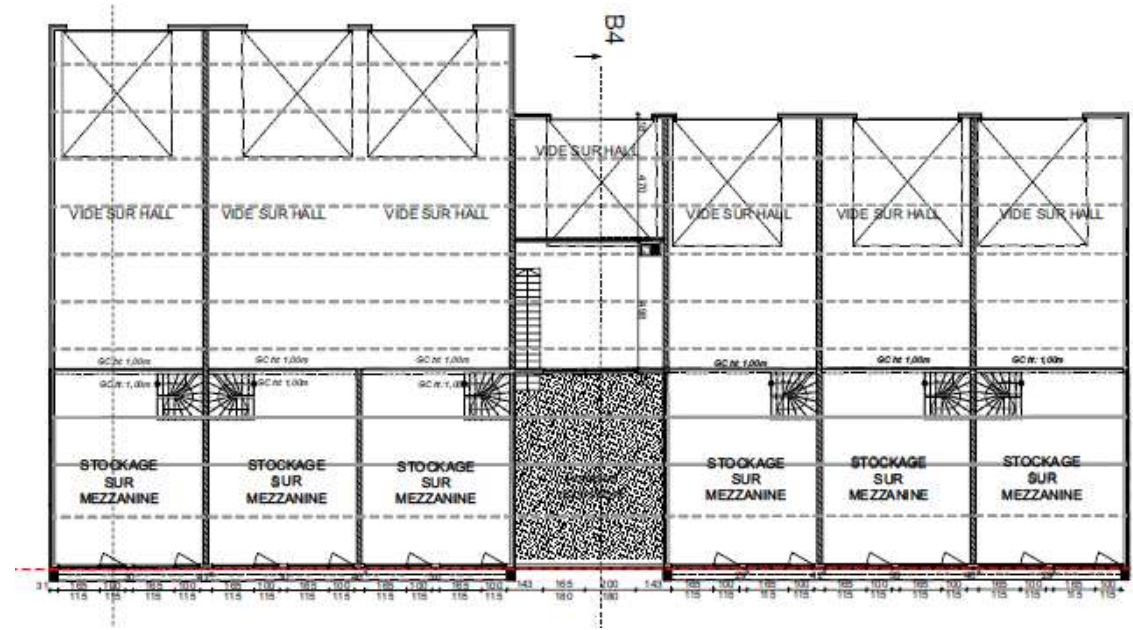


VUES EN PLAN

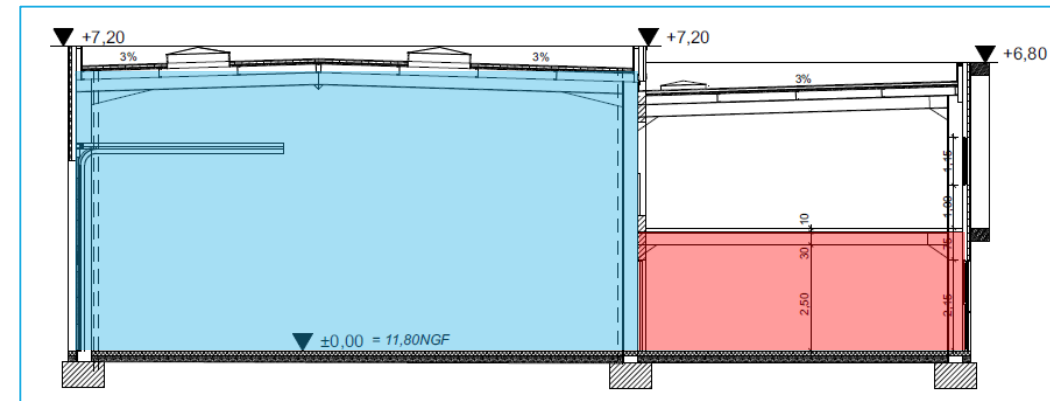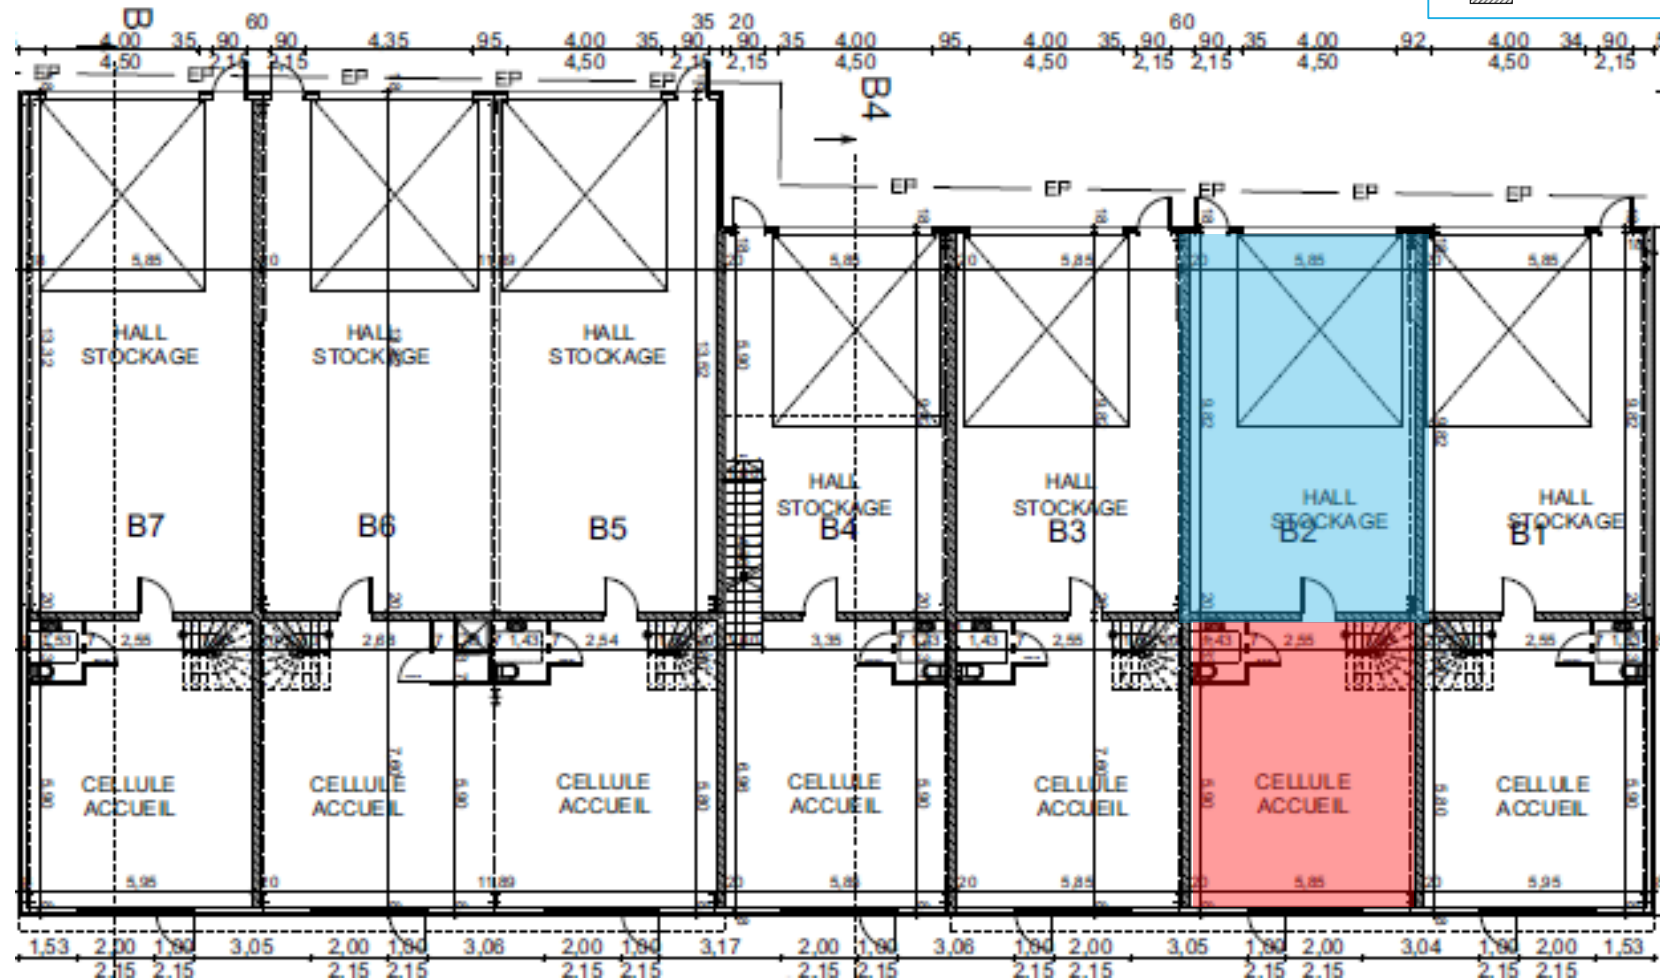



COUPE

VUES EN PLAN

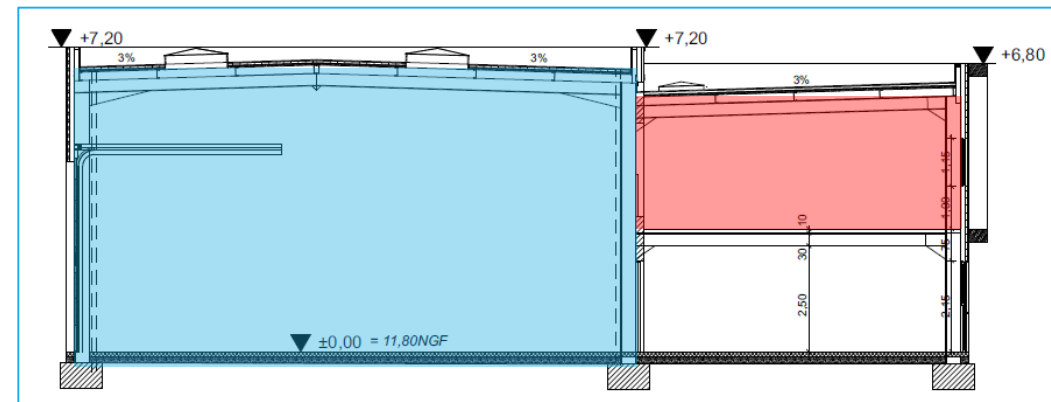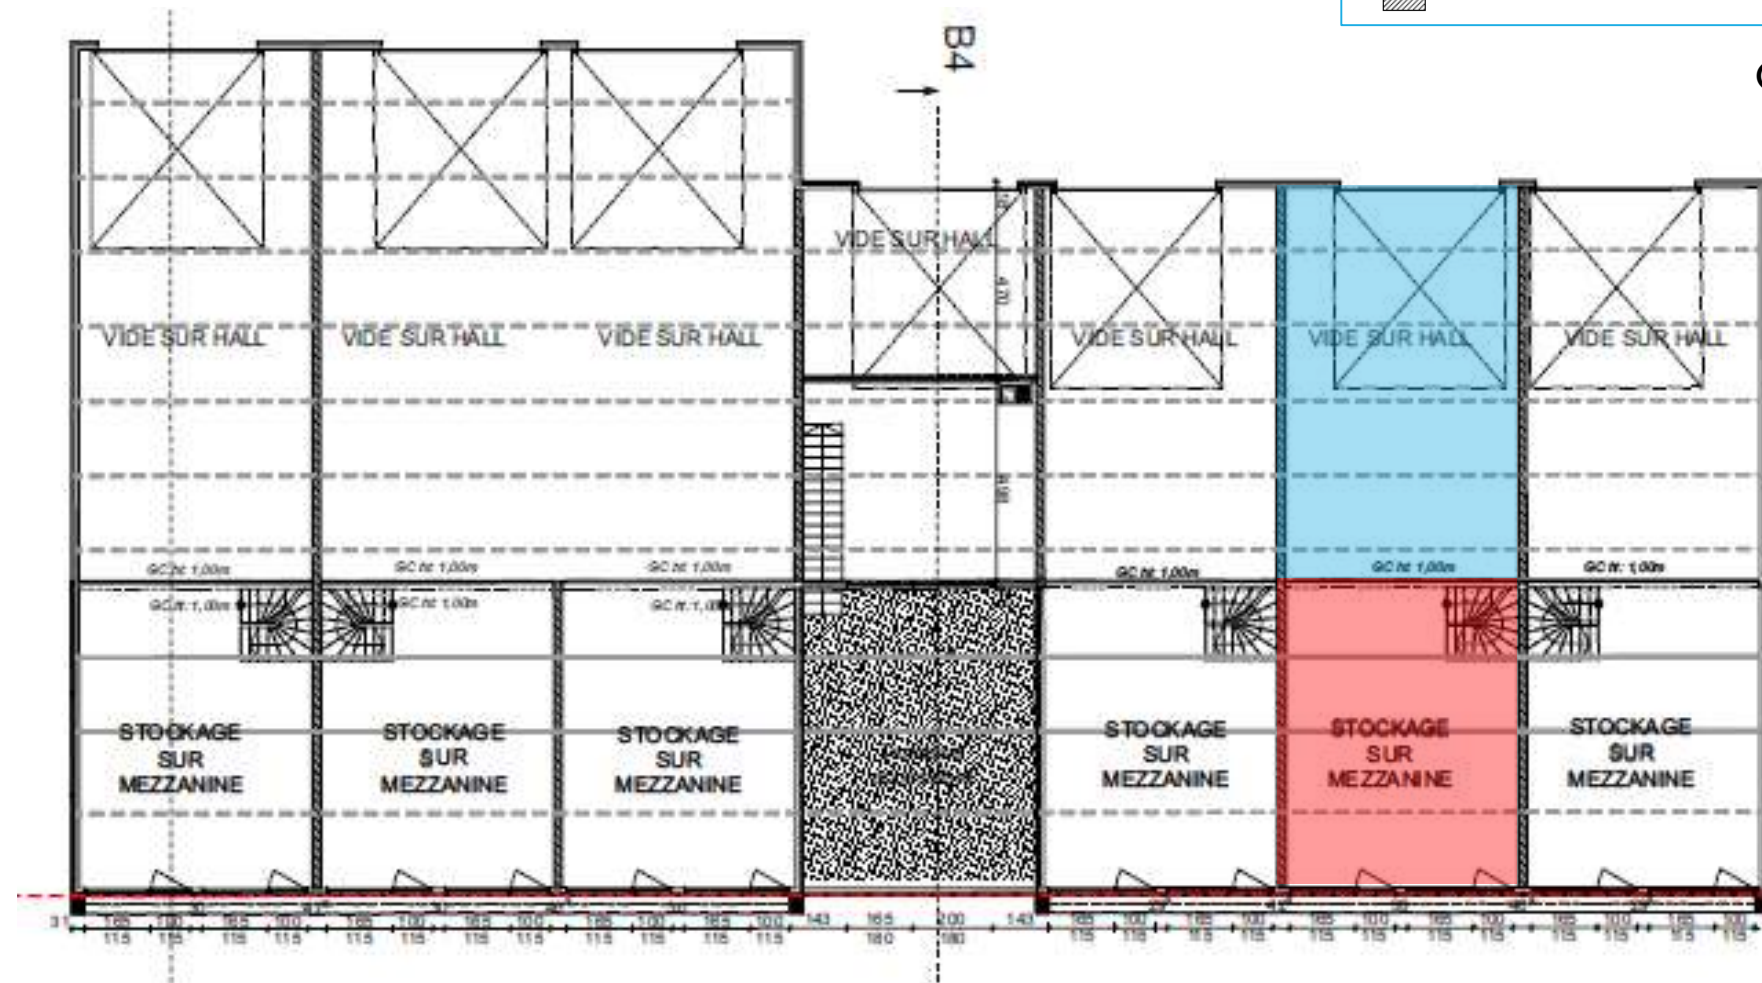

COUPE

COUPES

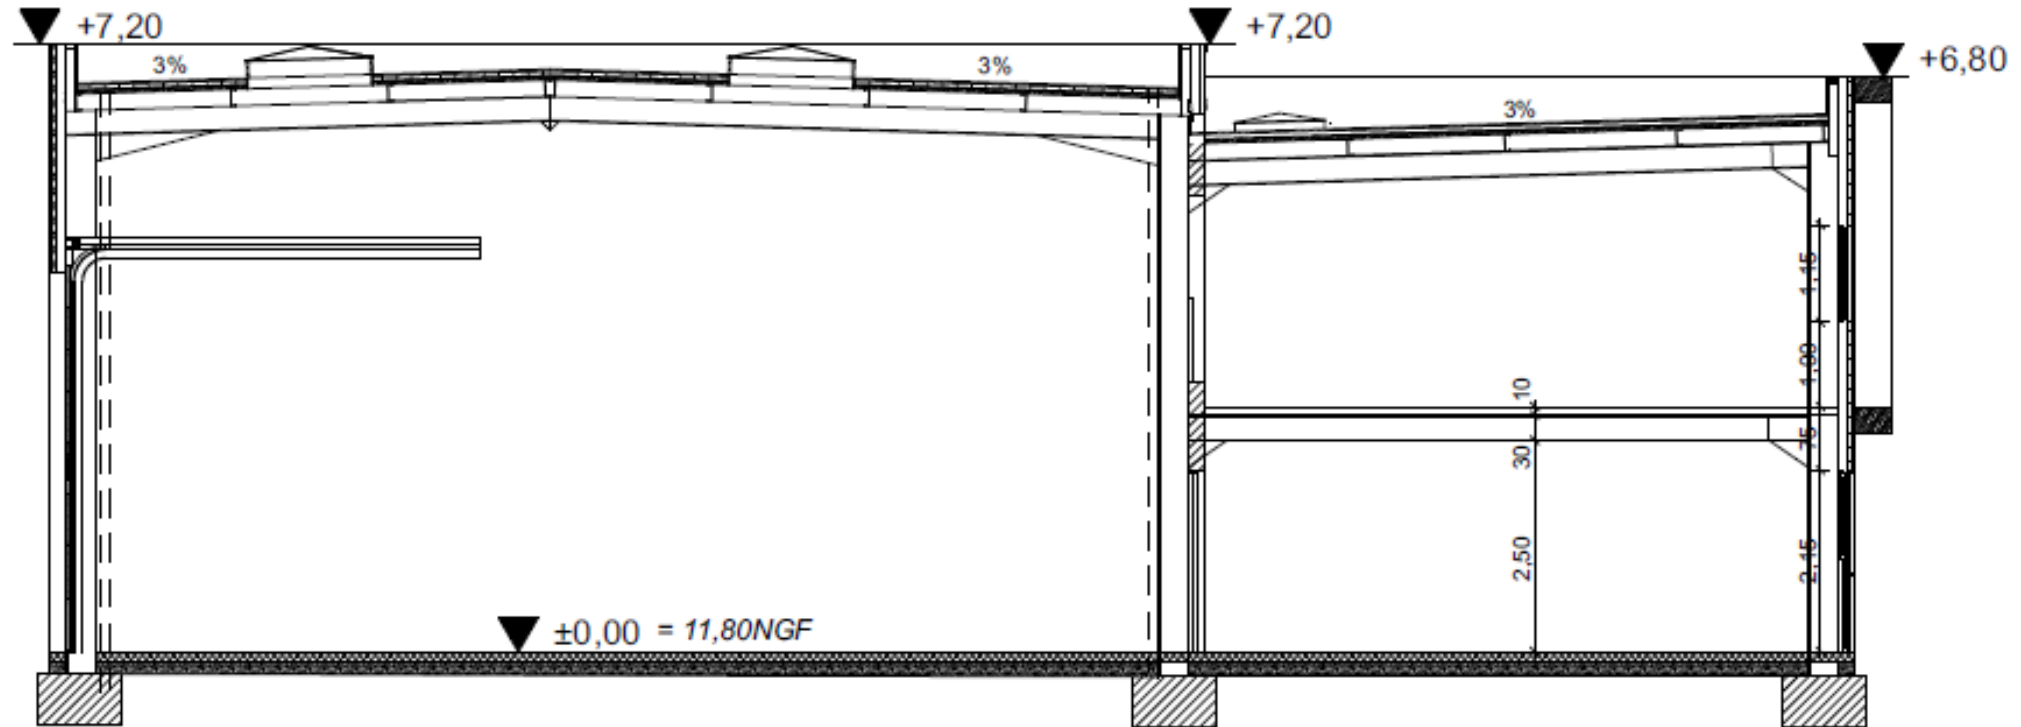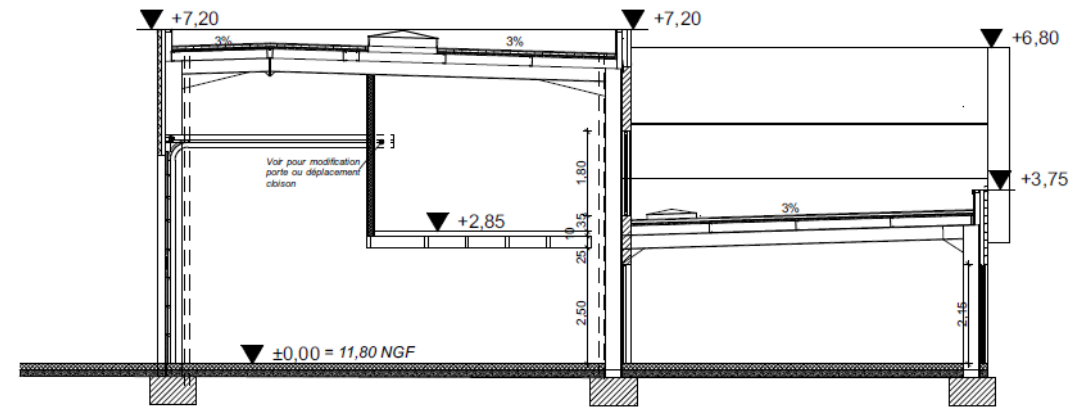

DÉROULEMENT

SÉANCES : 7 TD DE 4H

Séance de TD n°1 : repérages et synthèse (4h)

TRAVAIL INDIVIDUEL

Séance de TD n°2 et 3 :

- étude de la couverture, de l'étanchéité et de l'évacuation des eaux pluviales
- Bâtiment B

TRAVAIL INDIVIDUEL

Séance de TD n°4, 5, 6 et 7 :


- projet d'aménagement
- Cellule A9

TRAVAIL A FAIRE EN BINOME

Une évaluation MADOC est prévue lors de la dernière séance. Elle porte sur la connaissance du projet, les séances 1 2 et 3, la terminologie, l'utilisation des abaques, tableaux....

SUR MADOC :

	PRESENTATION DE LA SAE 2.1
	<u>SUJET</u>
	PLANS
	CCTP
	FONDS DE PLAN
	DTU 43.3
	DTU 60.11 part3 (EP)
	DTU 60.11 part2 (EU)
	BMI - SIPLAST

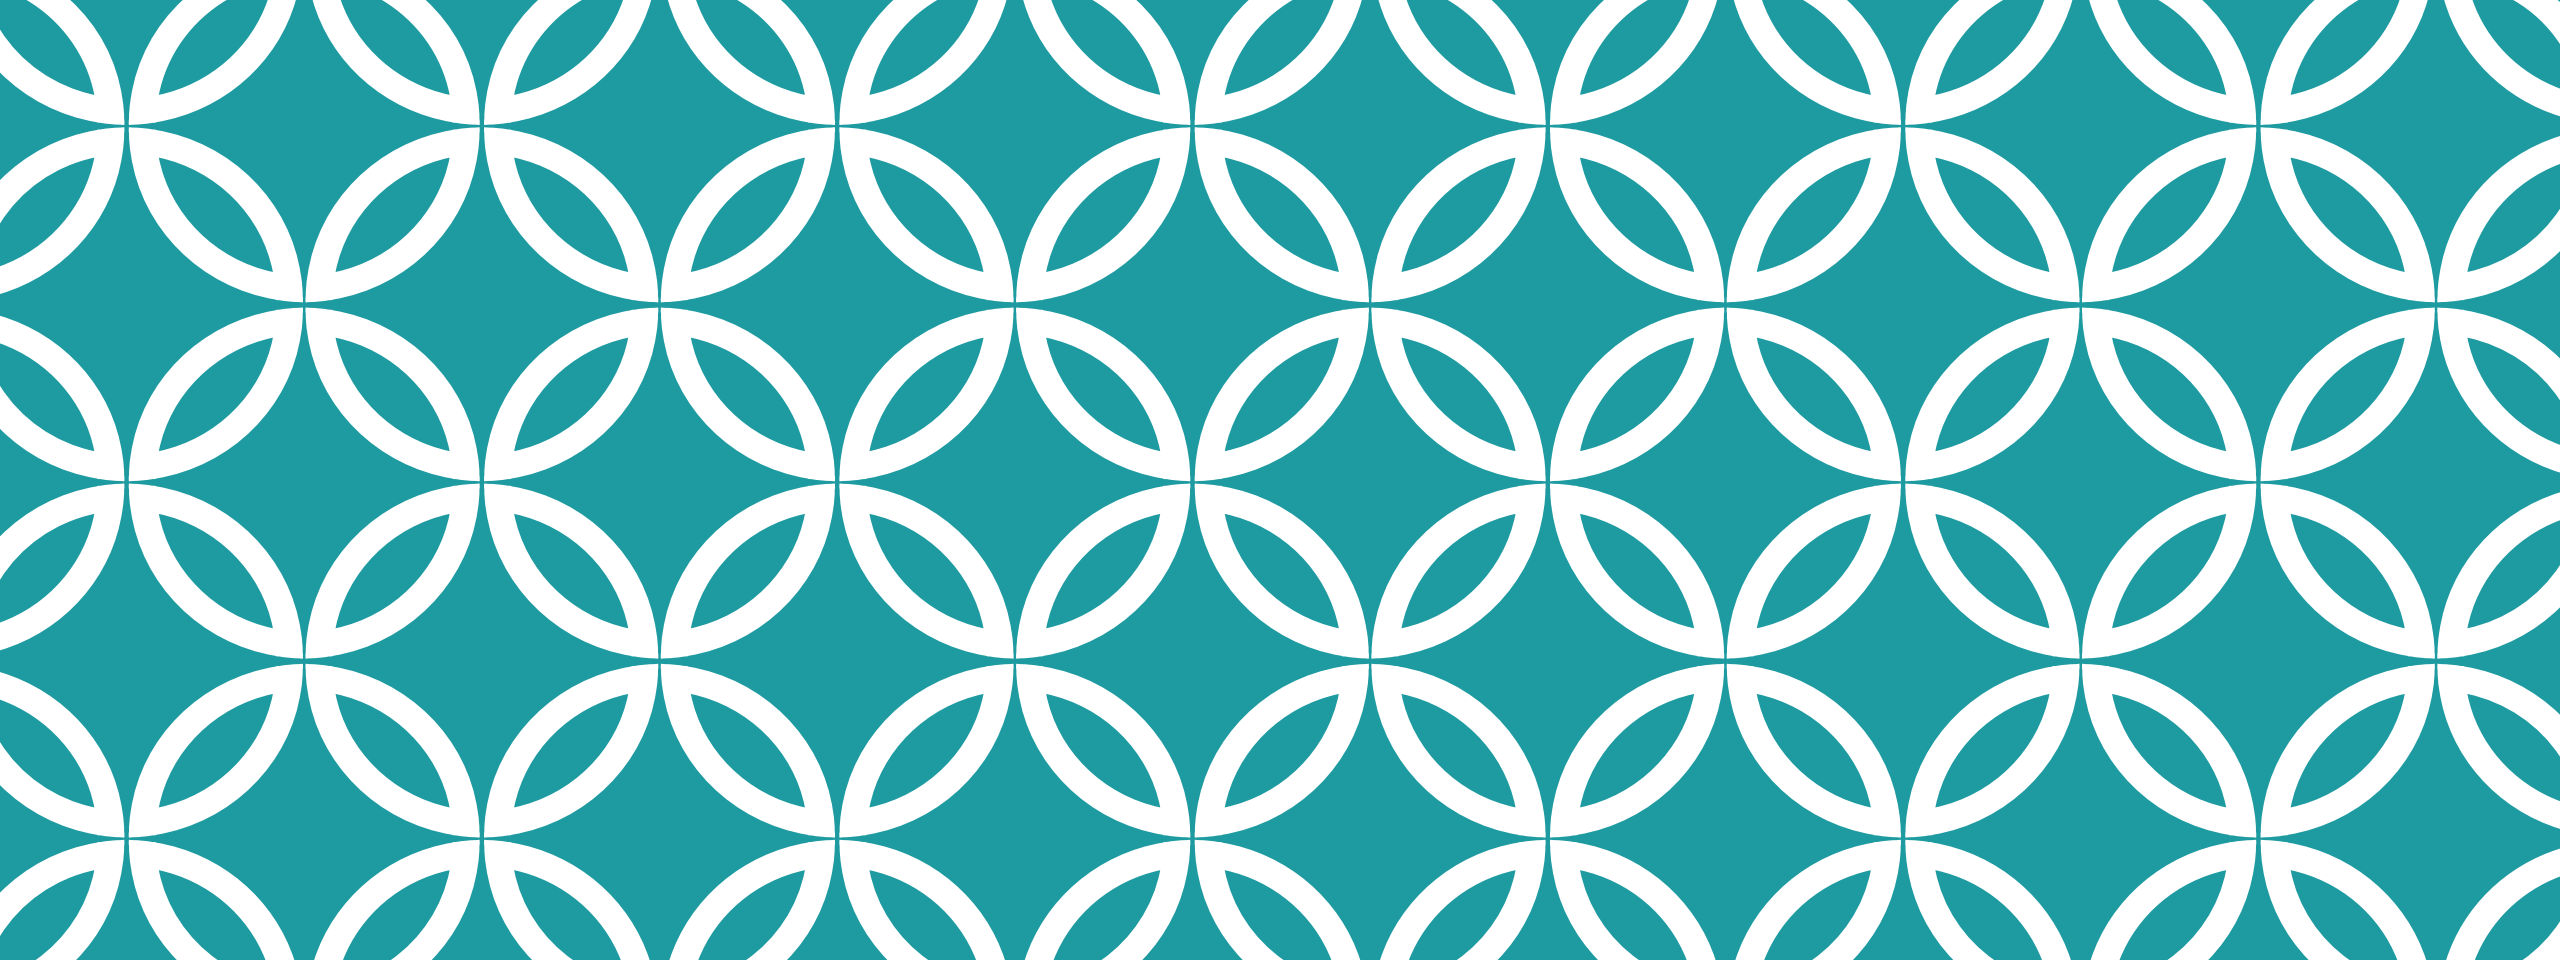


QUELQUES PHOTOS DU BÂTIMENT |

Façades principales des bâtiments

Panneaux sandwich



Aspect
« lisse »


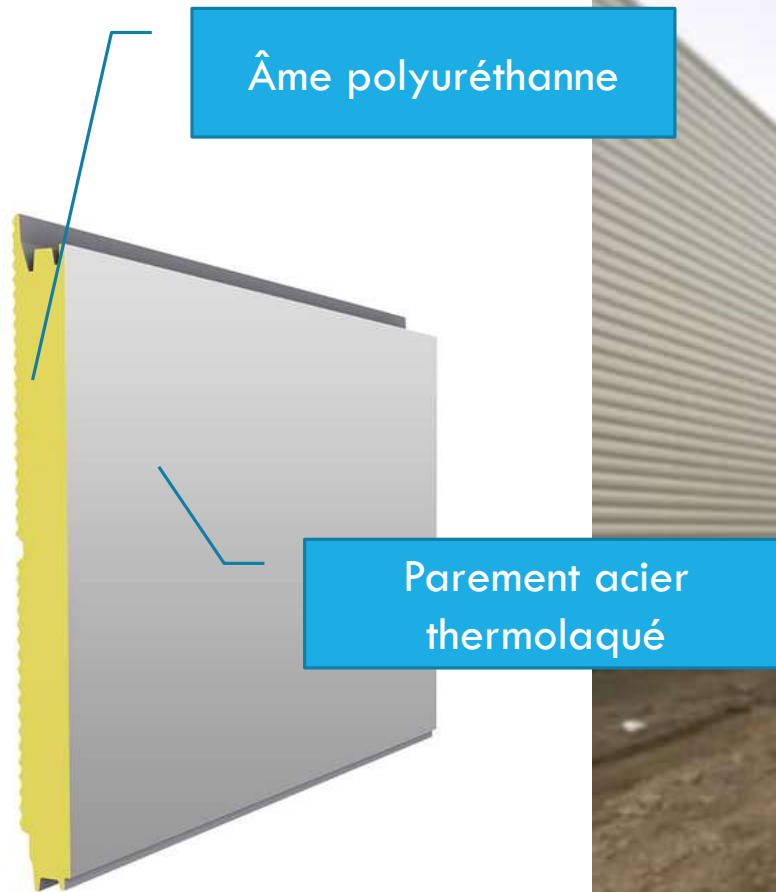


Assemblage
entre 2
panneaux



Façades arrières des bâtiments



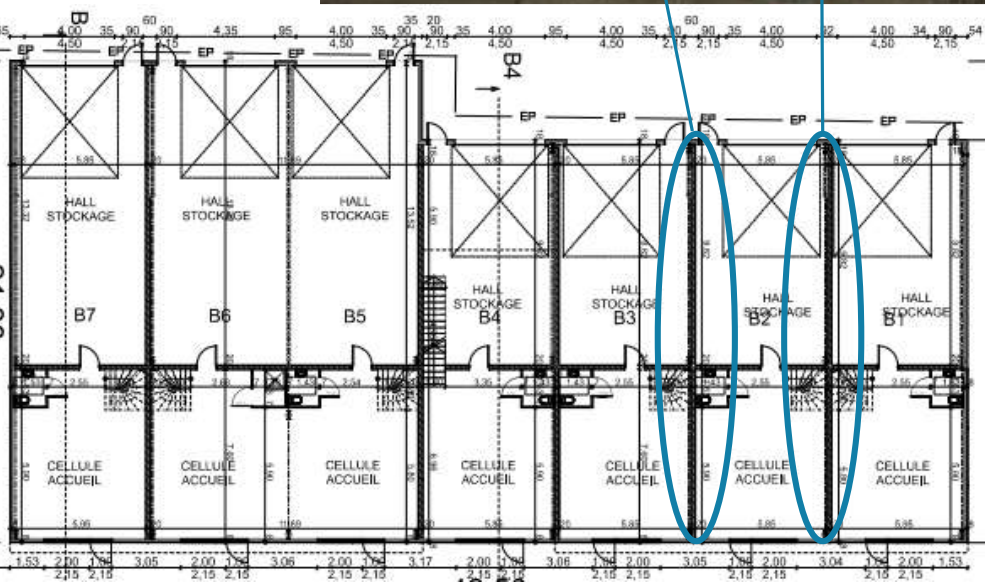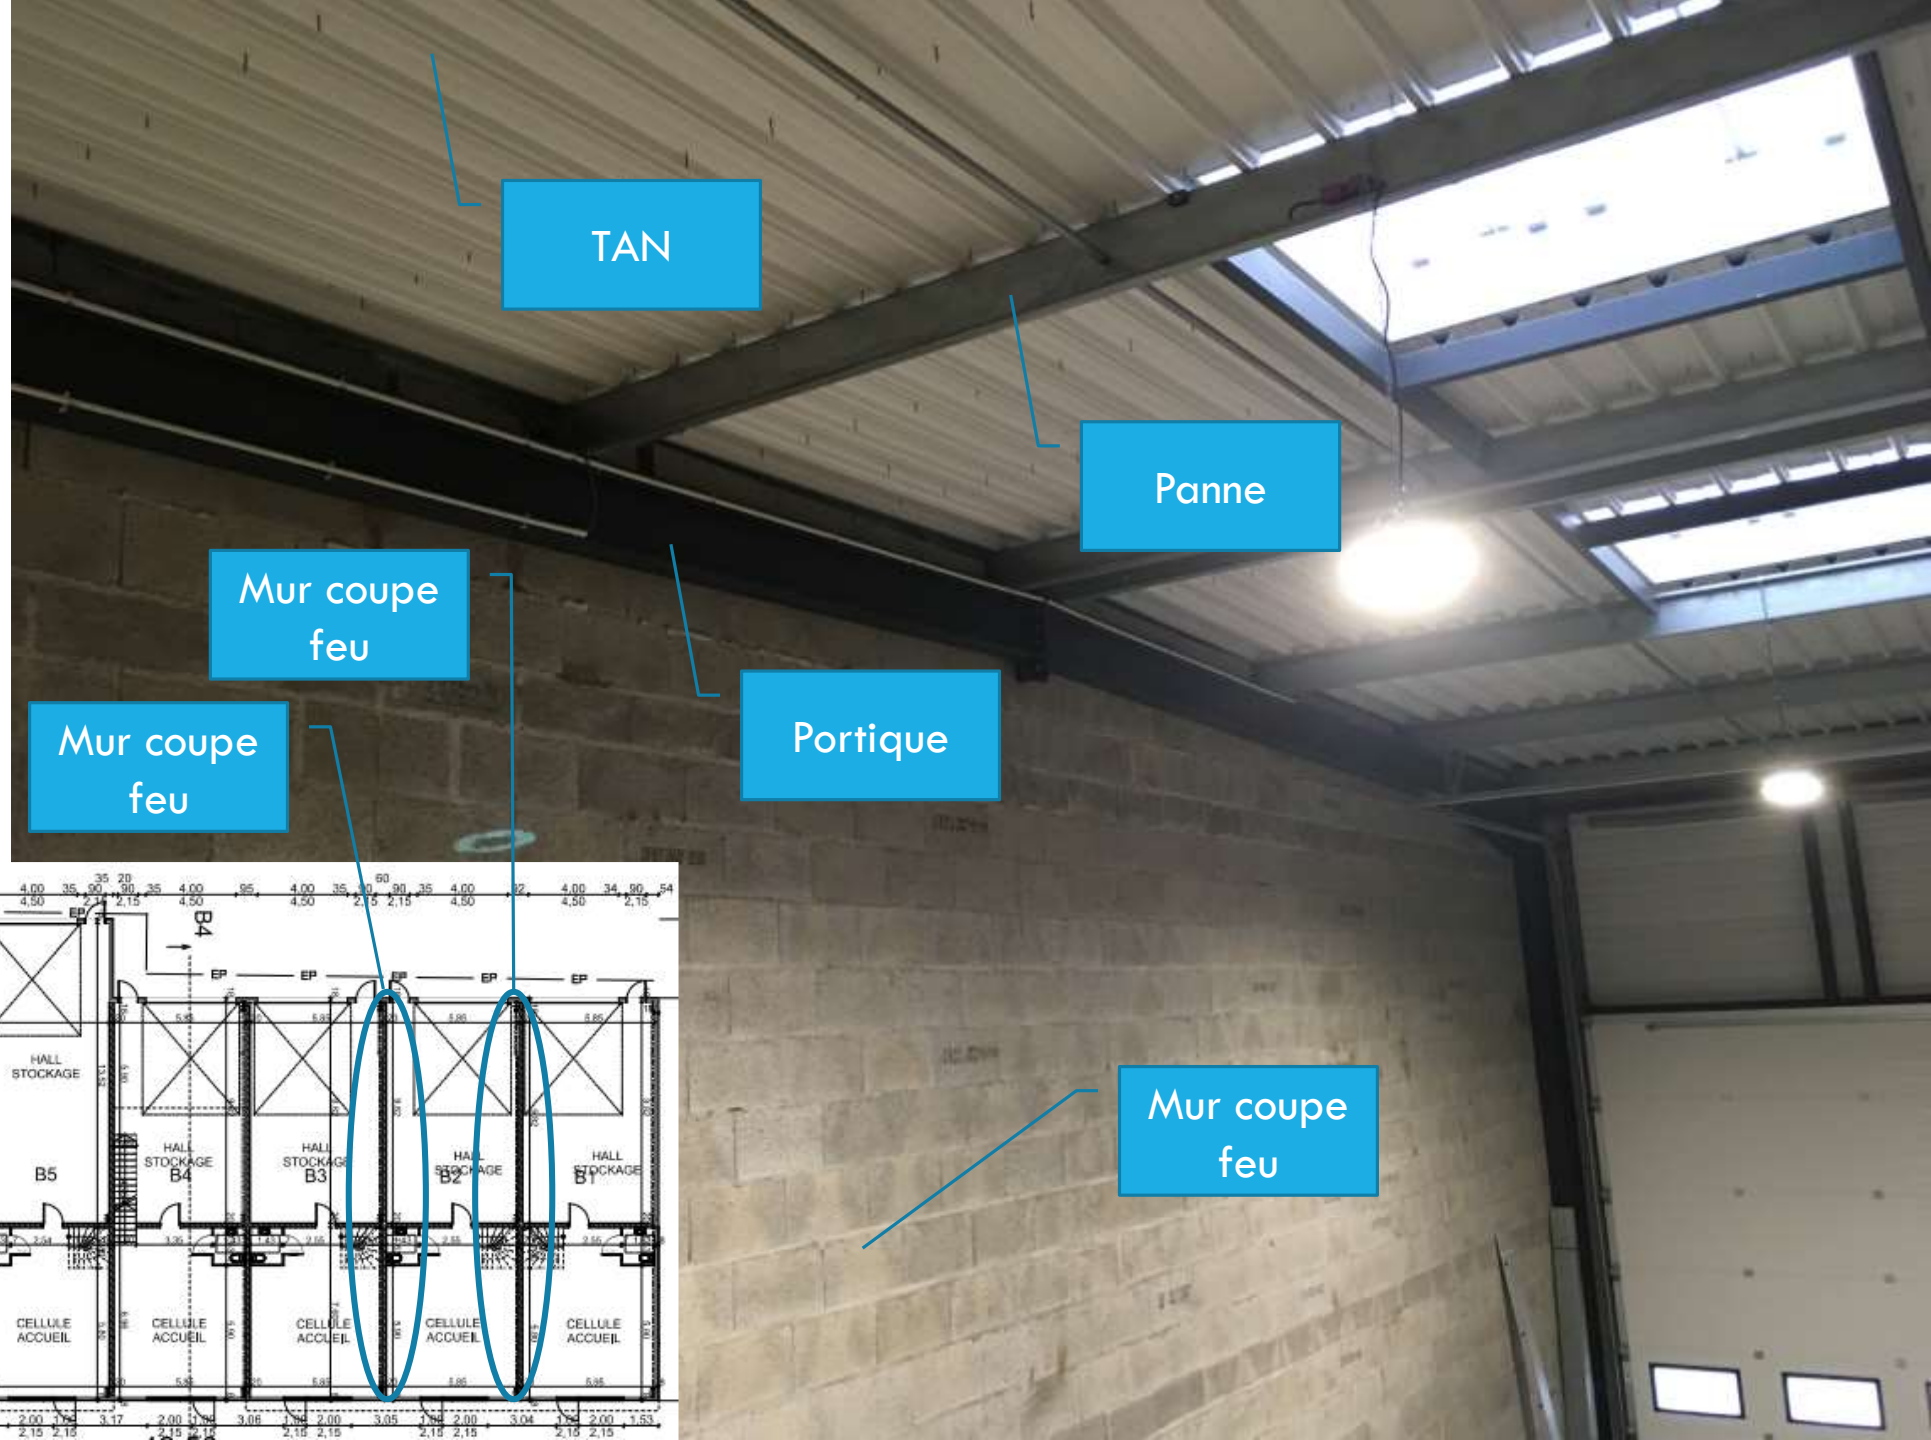



Portique

TAN


Une
« grande »
cellule


Dallage

Une
« petite »
cellule

Mur coupe
feu

Mur coupe
feu

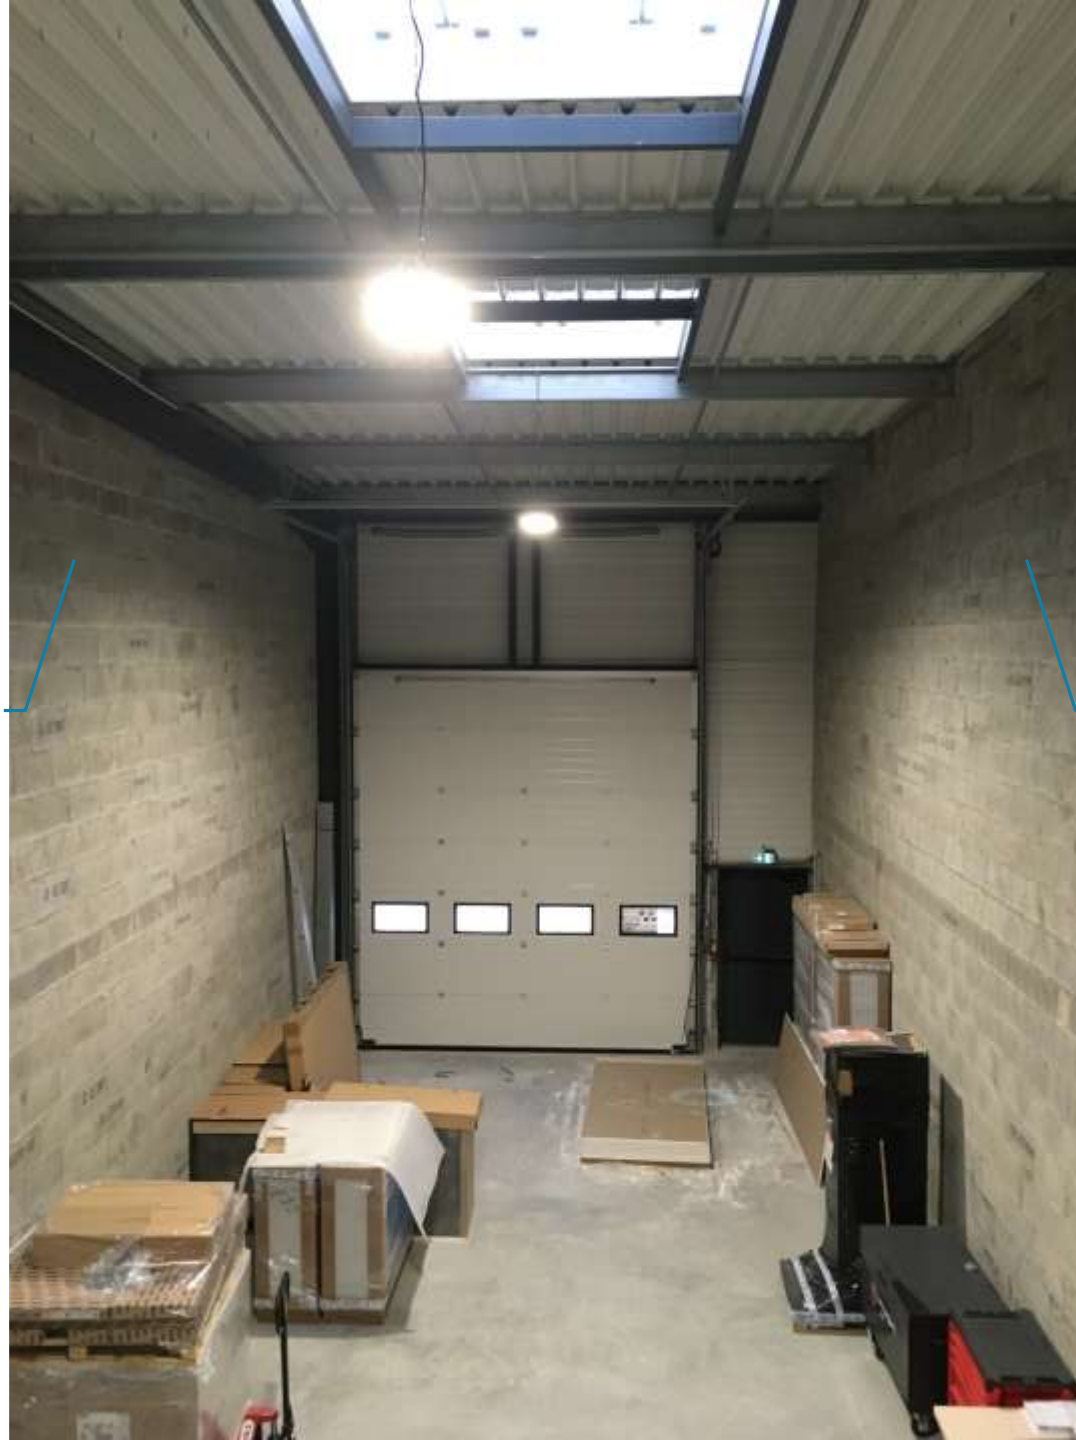

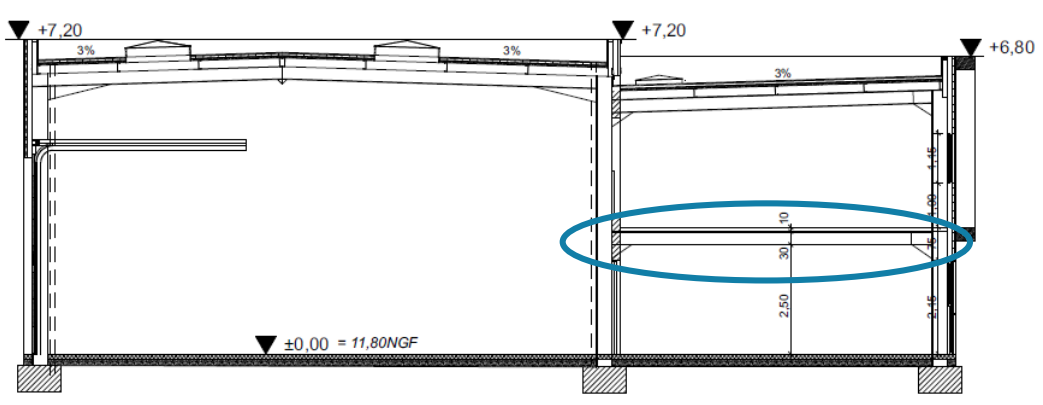

Plancher collaborant

Solive




Coulage du
dallage
surfacé



Coulage du
dallage
surfacé




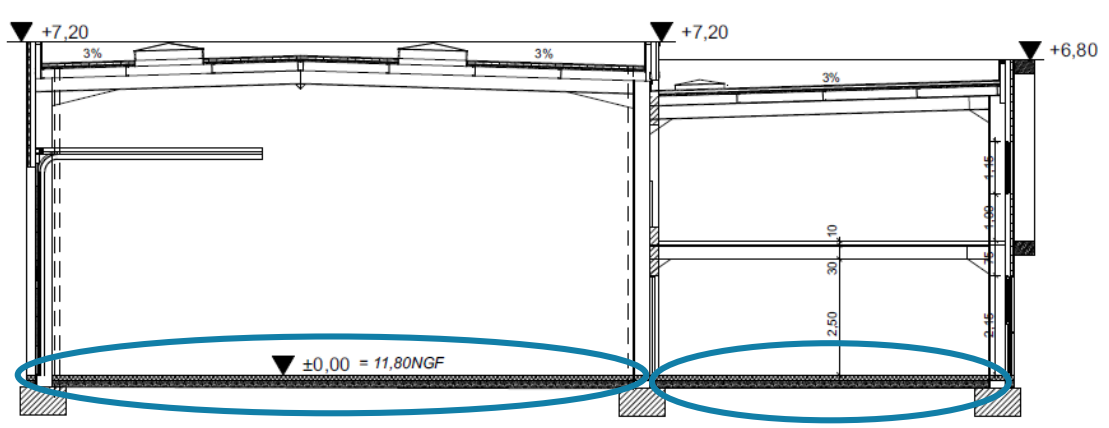

Coulage du
dallage
surfacé



Isolation des parois : ossature et isolant

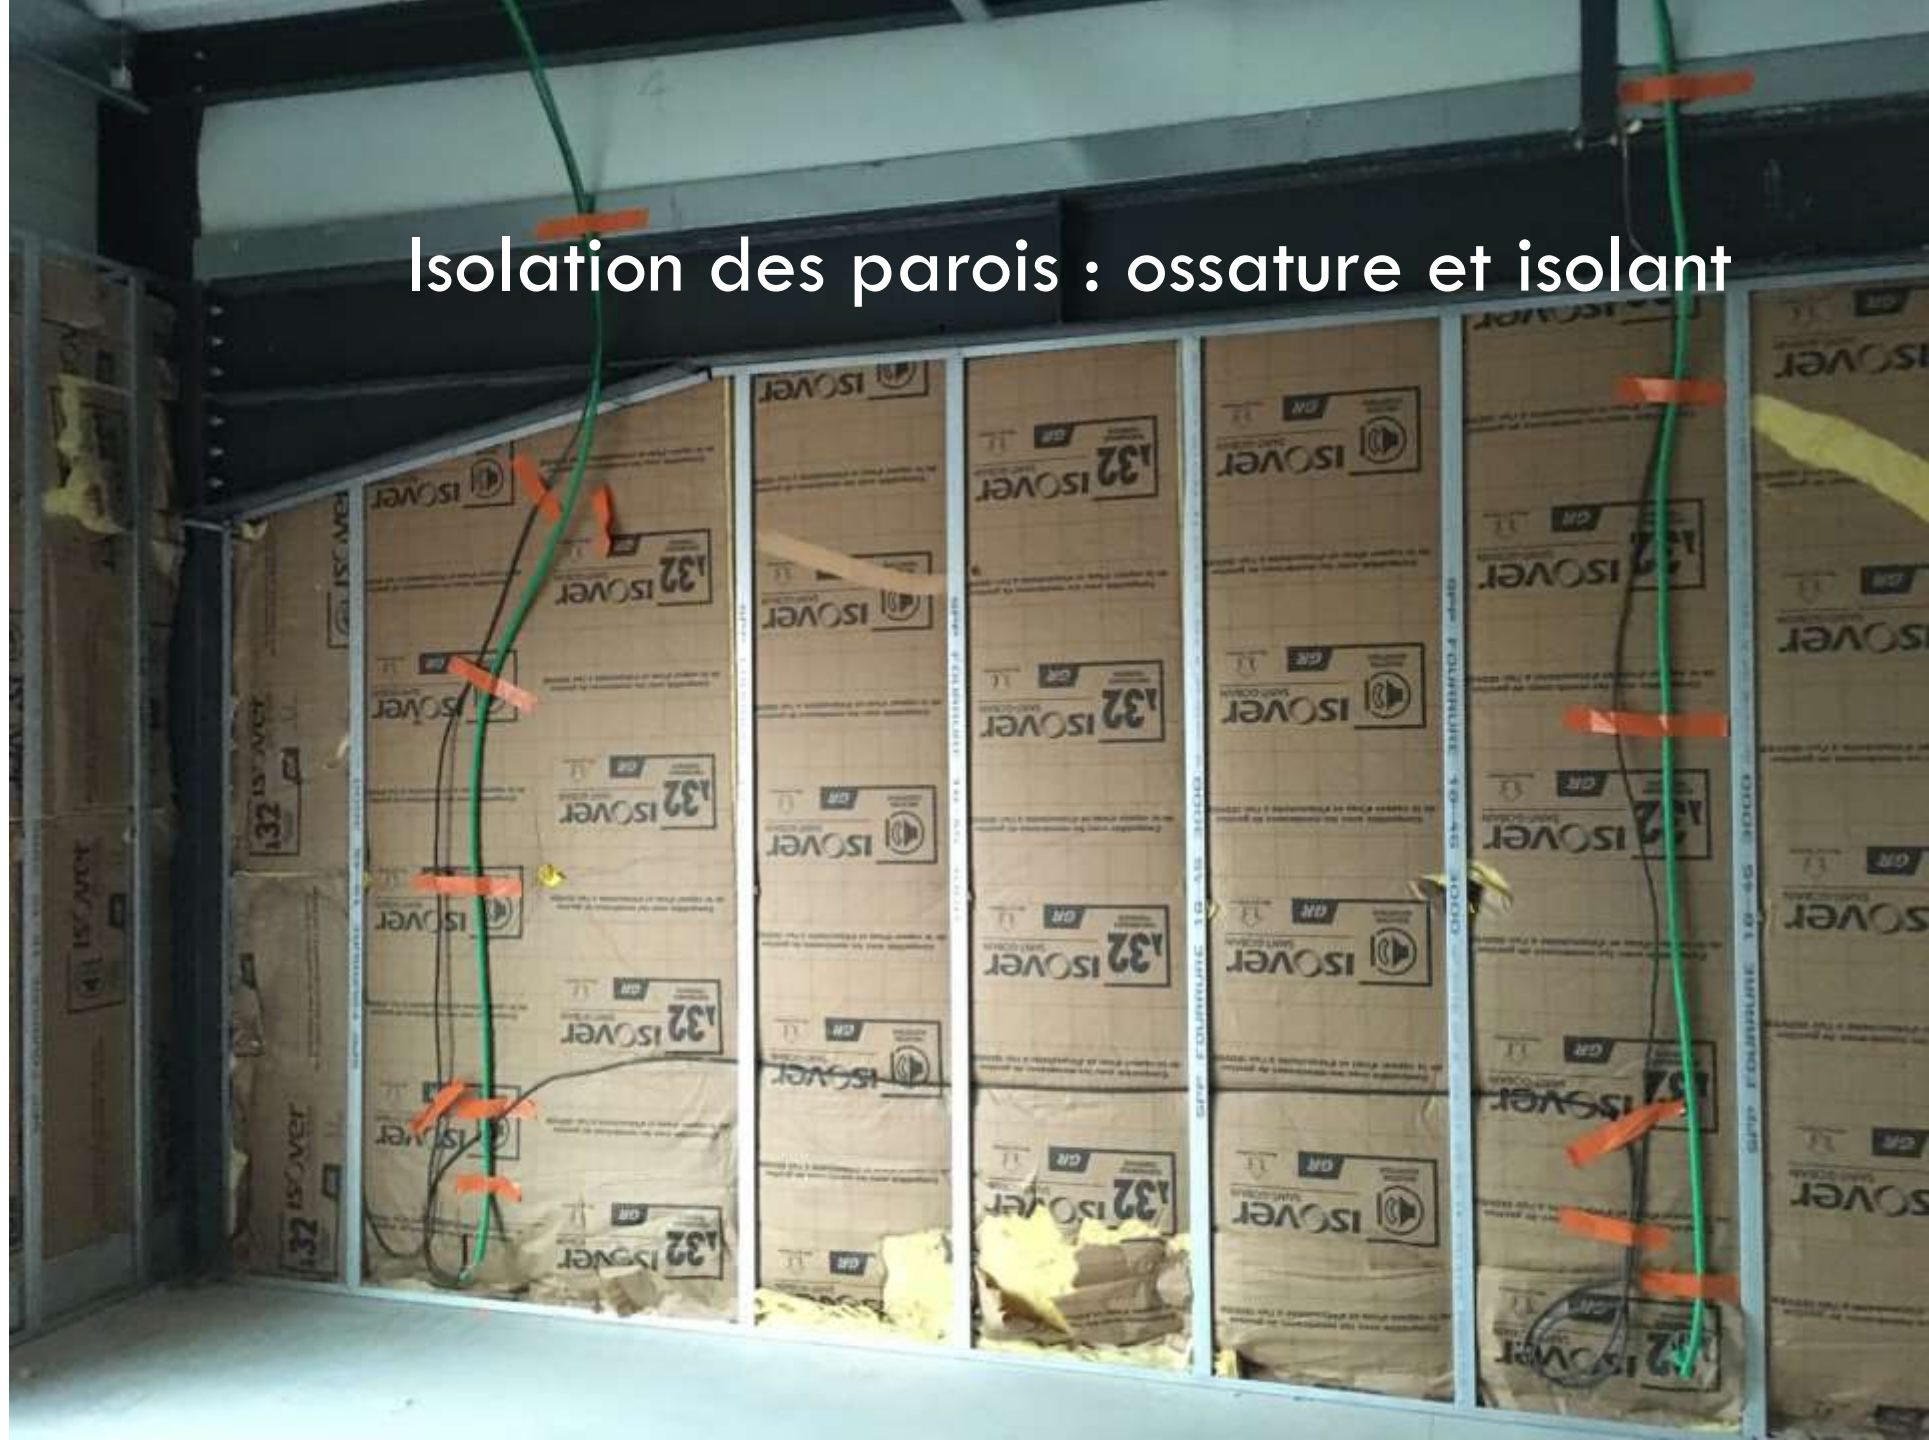

Isolation des parois : plaque de plâtre





Un aménagement
spécifique : création
d'une mezzanine dans
la partie « hall »





