

Dessinateur :

Jules LE GARS
Briac RAULT

Titre du document :

La Prinais
PLAN DE VOIERIE

Cotation :

m

Échelle :

1:1000



Lotissement de " La Prinais "

LEGENDE

- Voirie et plantations :
- Voirie en enrobé noir
- Cheminements piétons en bicouche beige
- Cheminements piétons en résine beige
- Bordures T1 ou T1 surbaissées
- Arase béton
- Emplacement place de parking en plaques alvéolées
- Gazon
- Plantations en massifs
- Arbres de haute tiges à planter
- Arbres de haute tige existants et à conserver
- Plantation de haie bocagère sur talus
- Plantation de haie vive composée d'au moins trois essences locales
- Possibilité de clore par un portail bois
- Sens de ruissellement
- 8.80

Cote de voirie finie
- 3

Numéro de profil en travers
- Changement pente, rampe
- Borne amovible
- Chasse-roue

Divers :

Candélabre (h=4,50m)

Candélabre avec protection type épingle

Accès double libre ouvert sur le domaine public

Accès double fixe ouvert sur le domaine public

Espace privatif non clos ouvert sur le domaine public

Coffrets EDF et GDF

Nota: pour les cheminements piétons en contact avec des massifs arbustifs, le revêtement en bicouche beige sera réalisé APRES la mise en place du film tissé

Dessinateur :

Jules LE GARS
Briac RAULT

Titre du document :

La Prinais
PLAN DE VOIERIE

Cotation :

m

Échelle :

1:1000

PLAN DE LA VOIRIE

Echelle :
1/1000

Lotissement de " La Prinais "


LEGENDE

Voirie et plantations :

- Voirie en enrobé noir
- Cheminements piétons en bicouche beige
- Cheminements piétons en résine beige
- Bordures T1 ou T1 surbaissées
- Arase béton
- Emplacement place de parking en plaques alvéolées
- Gazon
- Plantations en massifs
- Arbres de haute tiges à planter
- Arbres de haute tige existants et à conserver
- Plantation de haie bocagère sur talus
- Plantation de haie vive composée d'au moins trois essences locales
- Possibilité de clore par un portail bois
- Sens de ruissellement
- 8.80 Cote de voirie finie
- 3 Numéro de profil en travers
- Changement pente, rampe
- Borne amovible
- Chasse-route

Divers :

- Candélabre (h=4,50m)
- Candélabre avec protection type épingle
- Accès double libre ouvert sur le domaine public
- Accès double fixe ouvert sur le domaine public
- Espace privatif non clos ouvert sur le domaine public
- Coffrets EDF et GDF

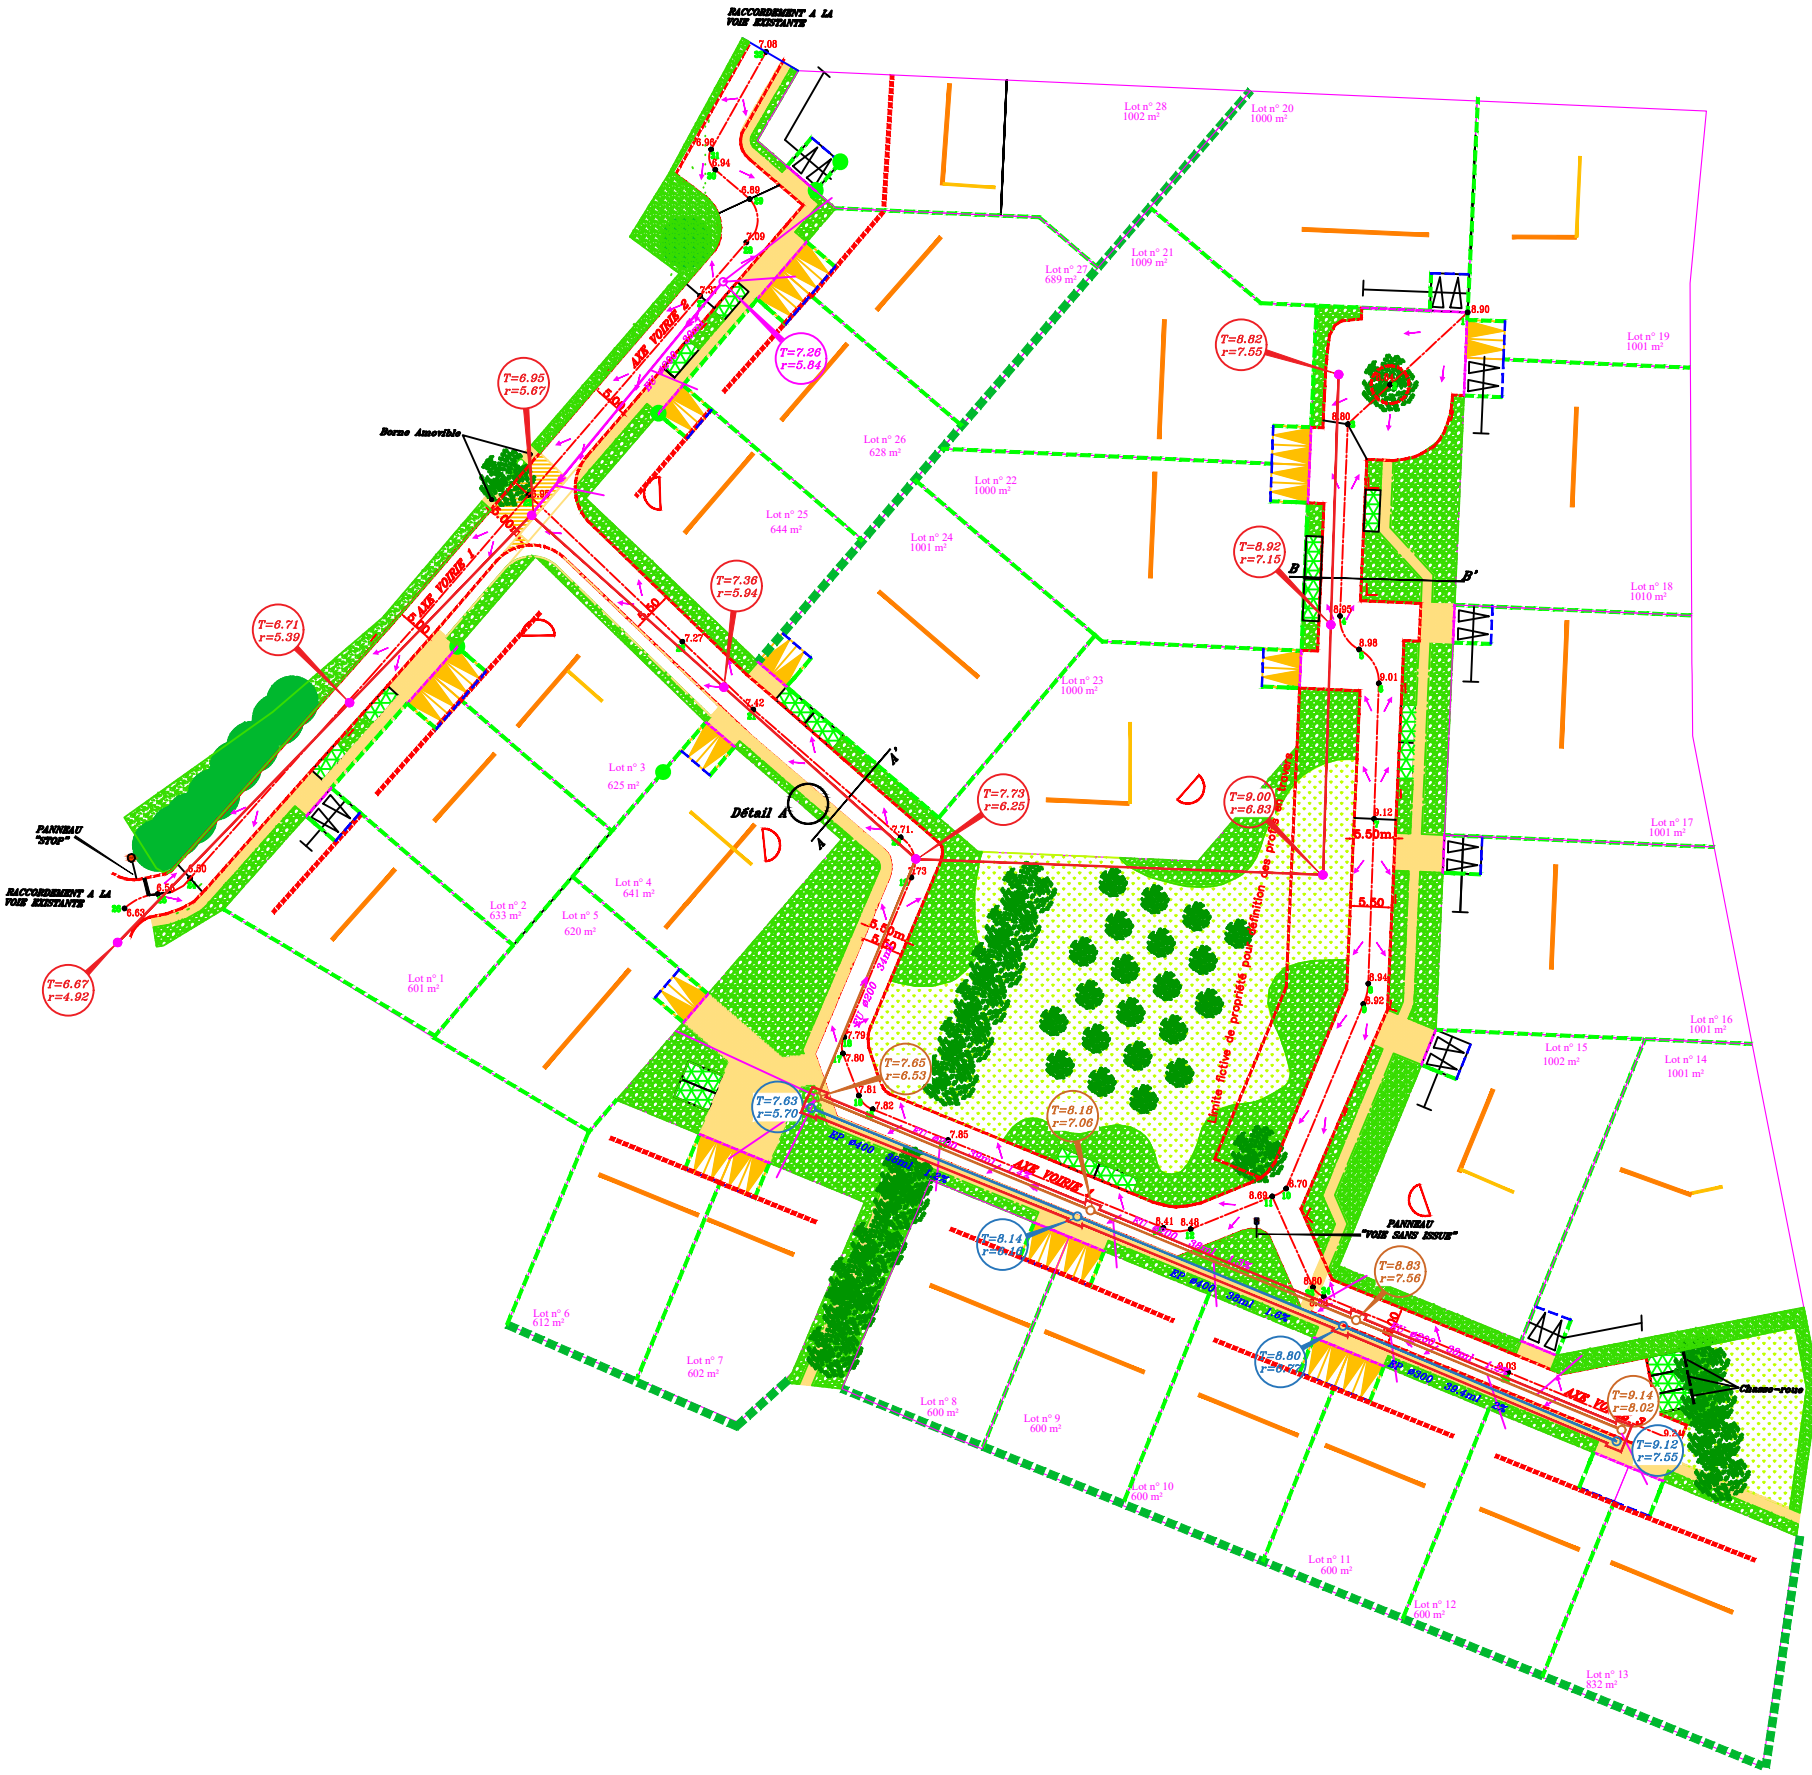

Nota: pour les cheminements piétons en contact avec des massifs arbustifs, le revêtement en bicouche beige sera réalisé APRES la mise en place du film tissé

Dessinateur :

Jules LE GARS
Briac RAULT

Titre du document :

La Prinais
PLAN DE VOIRIE

Cotation :

m

Échelle :

1:1000

PLAN DE LA VOIRIE

Echelle :
1/1000

Lotissement de " La Prinais "

LEGENDE

Voirie et plantations :

- Voirie en enrobé noir
- Cheminements piétons en bicouche beige
- Cheminements piétons en résine beige
- Bordures T1 ou T1 surbaissées
- Arase béton
- Emplacement place de parking en plaques alvéolées
- Gazon
- Plantations en massifs
- Arbres de haute tiges à planter
- Arbres de haute tige existants et à conserver
- Plantation de haie bocagère sur talus
- Plantation de haie vive composée d'au moins trois essences locales
- Possibilité de clore par un portail bois
- Sens de ruissellement
- 8.80


Cote de voirie finie
- 3

Numéro de profil en travers
- Changement pente, rampe
- Borne amovible
- Chasse-roue

Divers :

- Candélabre (h=4,50m)
- Candélabre avec protection type épingle
- Accès double libre ouvert sur le domaine public
- Accès double fixe ouvert sur le domaine public
- Espace privatif non clos ouvert sur le domaine public
- Coffrets EDF et GDF

Nota: pour les cheminements piétons en contact avec des massifs arbustifs, le revêtement en bicouche beige sera réalisé APRES la mise en place du film tissé

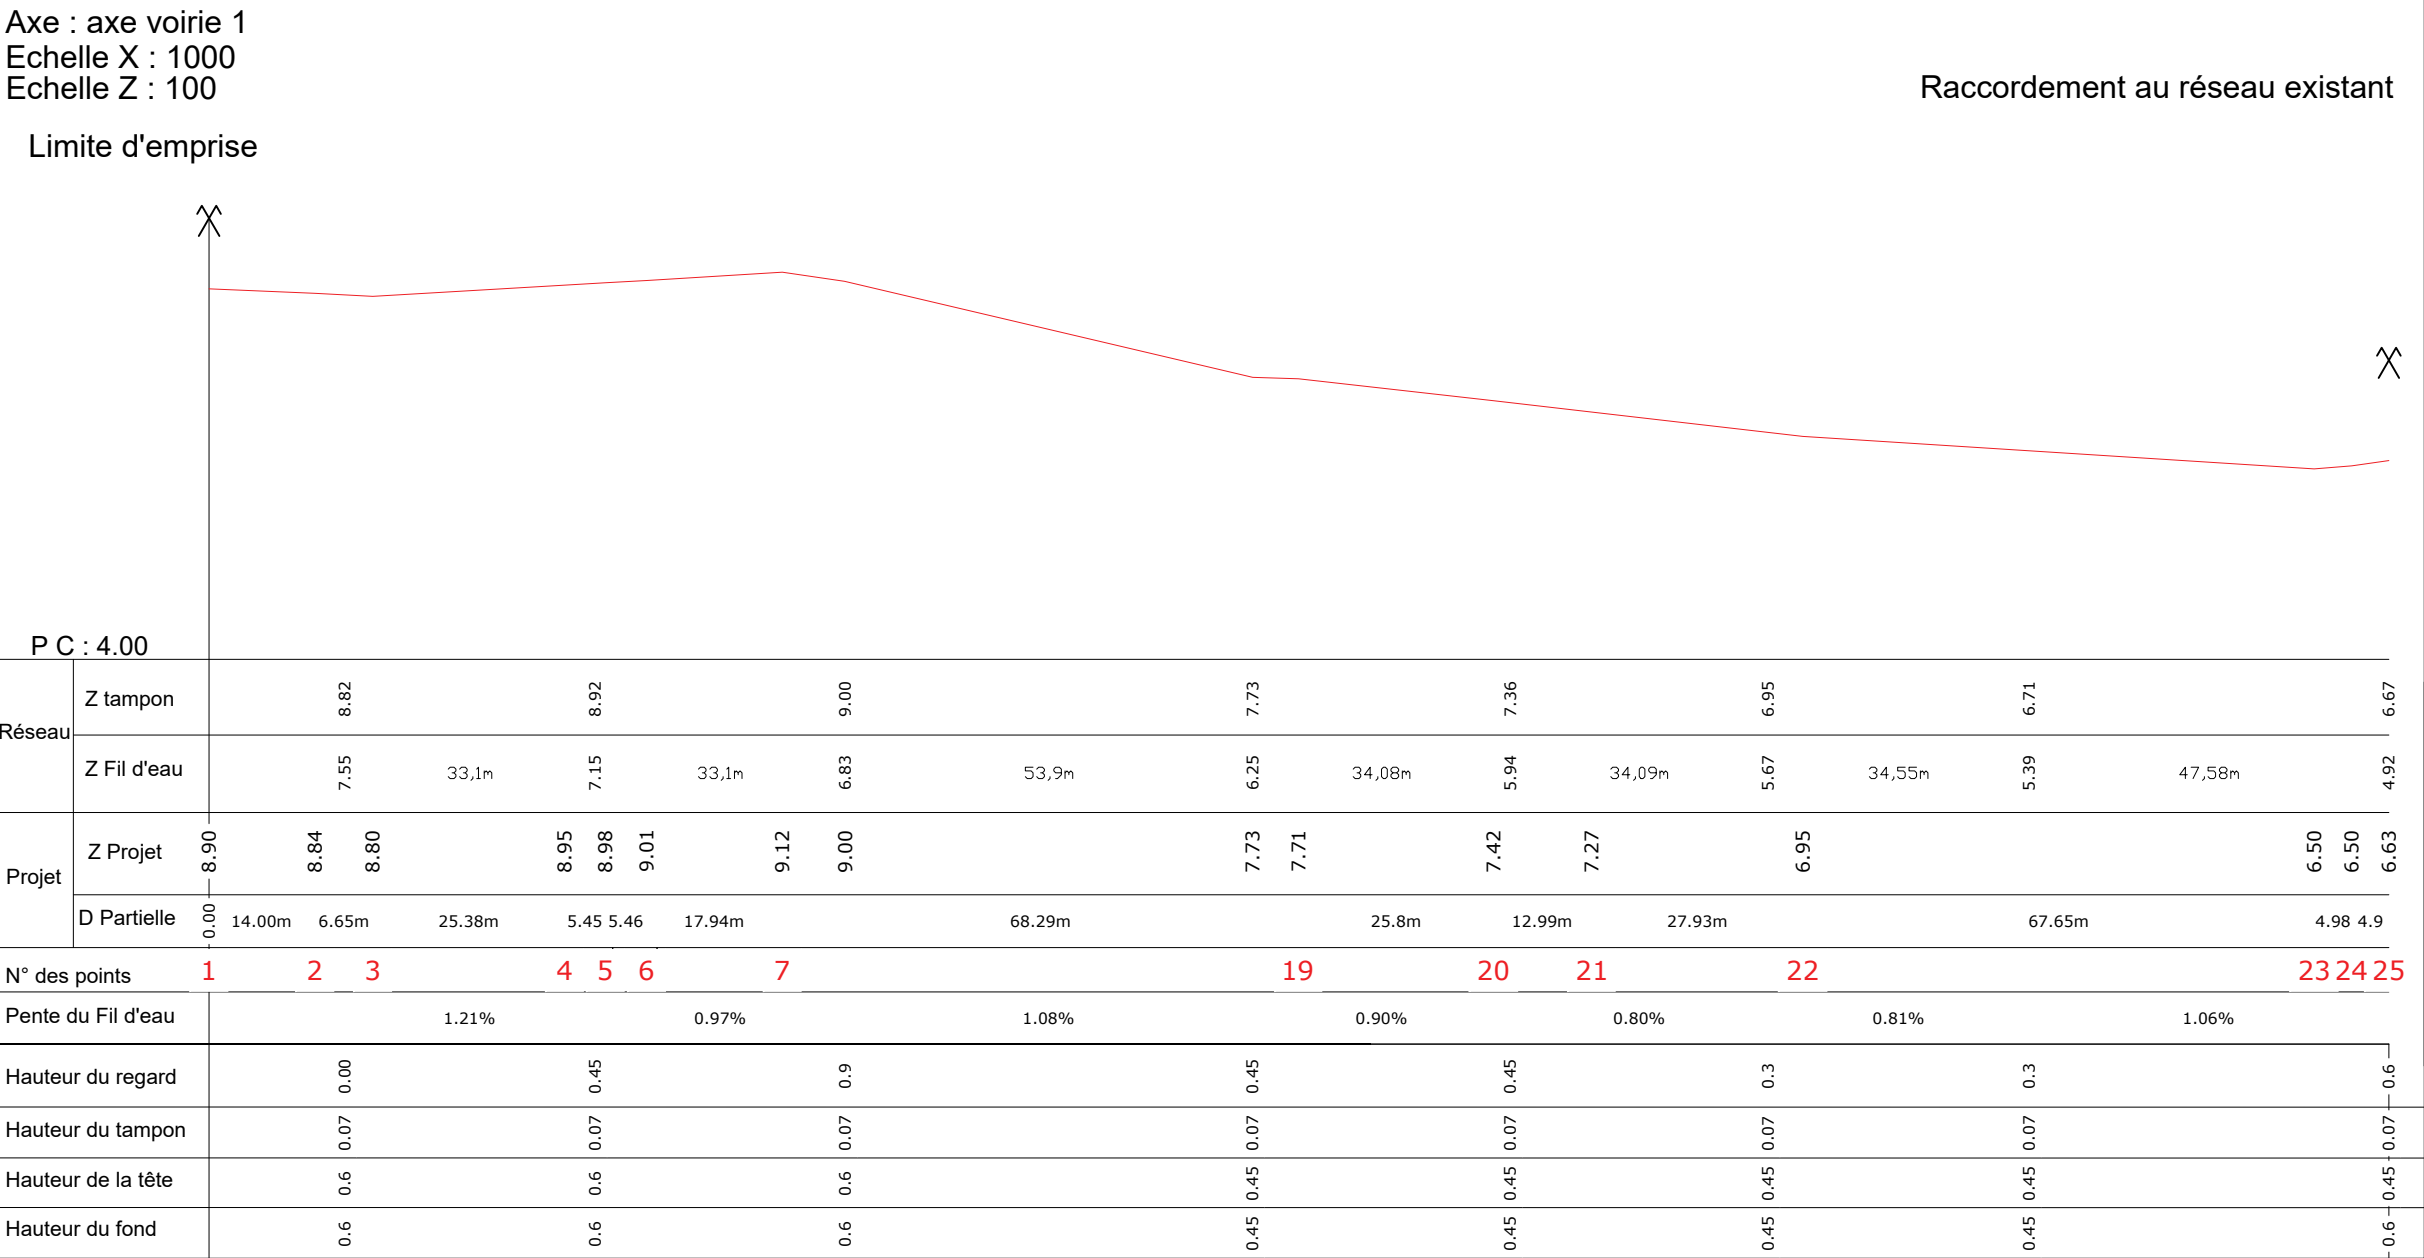

Dessinateur :

Jules LE GARS
Briac RAULT

Titre du document :


La Prinais
PLAN DE VOIERIE

Cotation :

m

Axe : Voirie 1
N° profil : P 15
Pk : 108.27m

P C : 5.0

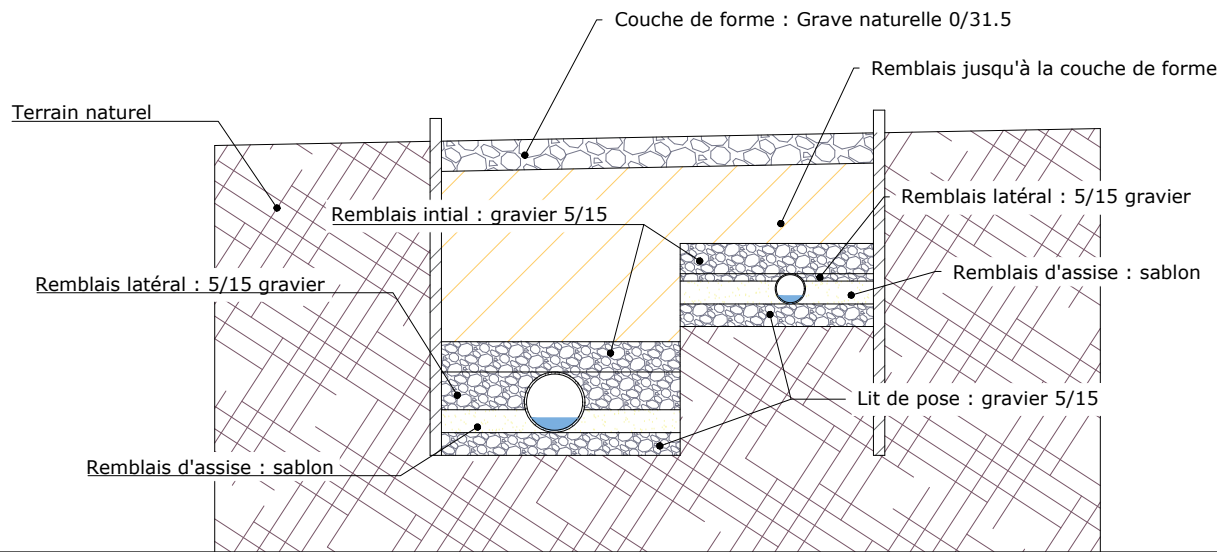

Dessinateur :
Jules LE GARS Briac RAULT
Titre du document :
La Prinais PLAN DE VOIERIE
Cotation :
<i>m</i>
Échelle :
1:50