


Lotissement de la Prinai

Axe : Voirie 1
N° profil : P 22
Pk : 264.30 m

Echelle X : 1/100
Echelle Z : 1/100

Z Tn :
Z Projet :
P C : 5.0

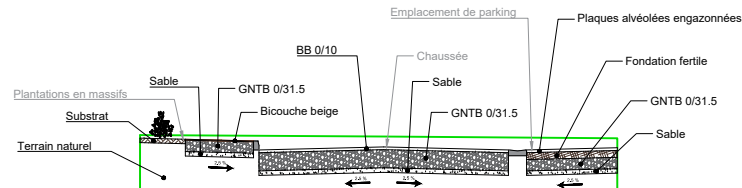

Dessinateur :

Jules LE GARS

Échelle :

1:100

Terrain	7.53			7.50		7.46
	7.23			7.20		7.16
	7.46	7.43	7.40	7.27	7.20	7.25
	7.36	7.06	6.64	6.71	6.64	6.69

Surface Décapage	1.4872	1.5450	3.16 m ²	20.55 m	64.9 m ³
Surface Déblais	0.2778	2.9800	4.37 m ²		89.8 m ³
Surface Remblais	0.1238		0.12 m ²		2.5 m ³
Surface totales				Longueur d'application	Volumes